

# PORT FOLIO

**Presented By : Shruti Koolwall**

*Interior Designer*

# ABOUT



*Shruti Koolwal*

Interior Designer, graduated with B.Des degree in the year 2023, possess a fruitful work experience of more than one and a half year in the industry and looking forward to learn and explore the different segments of the field along with some established Designers and Architects.

# OVERVIEW

-About

-Overview

-3BHK Residential (Ashiana Umang)

-4BHK Residential (Ms. Verma)

-Showroom (Aaditya Bath)

-Satyam House (Residential)

-Ajay Villa

-Somdatt Residency

-Amore Apartment (Gym)

# Full Home Residential Project - I

**Location - Block - 28, Aashiana Umang, Jhai, Rajasthan.**

**Area – 3.5 BHK (1787sq.ft.)**

This is a luxury apartment in a well renowned society of Jaipur.

Area comprises of 3 spacious Bedrooms and a Study/Mandir place. Along with a welcoming Living area attached to the Dining room and an Open Kitchen.

Client, being a person with high social station and a family man at the same time, required a cozy & soothing space for his family and place to have gatherings and get-togethers too.

## Scope -



- Modular Kitchen
- Modular Wardrobe & Storages
- Furniture
- Civil work
- Services



## Bedrooms




**Parent's Bedroom**

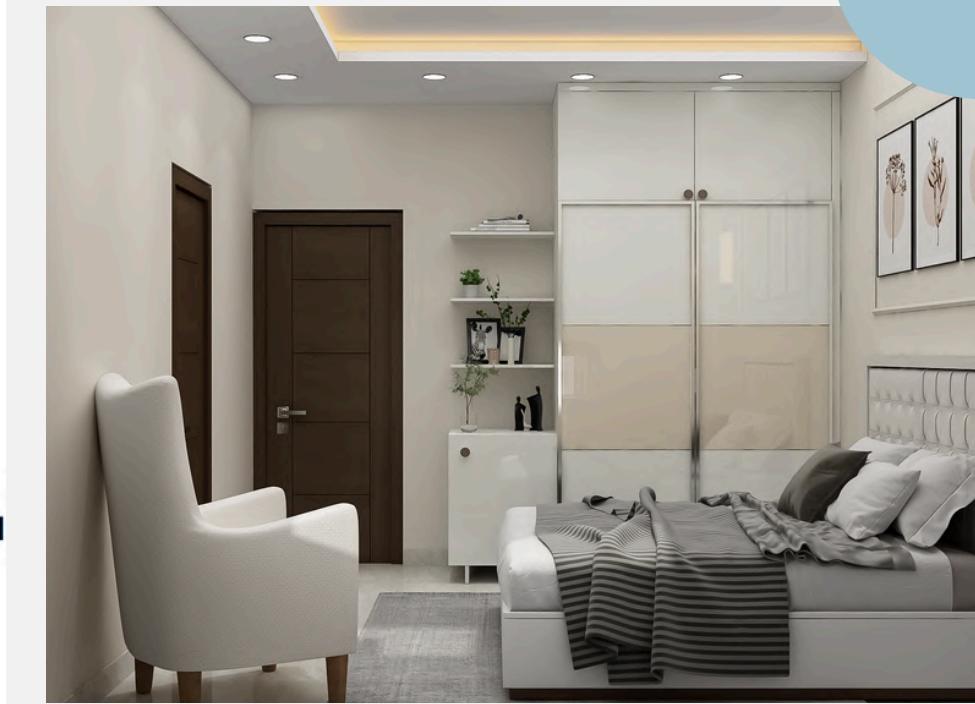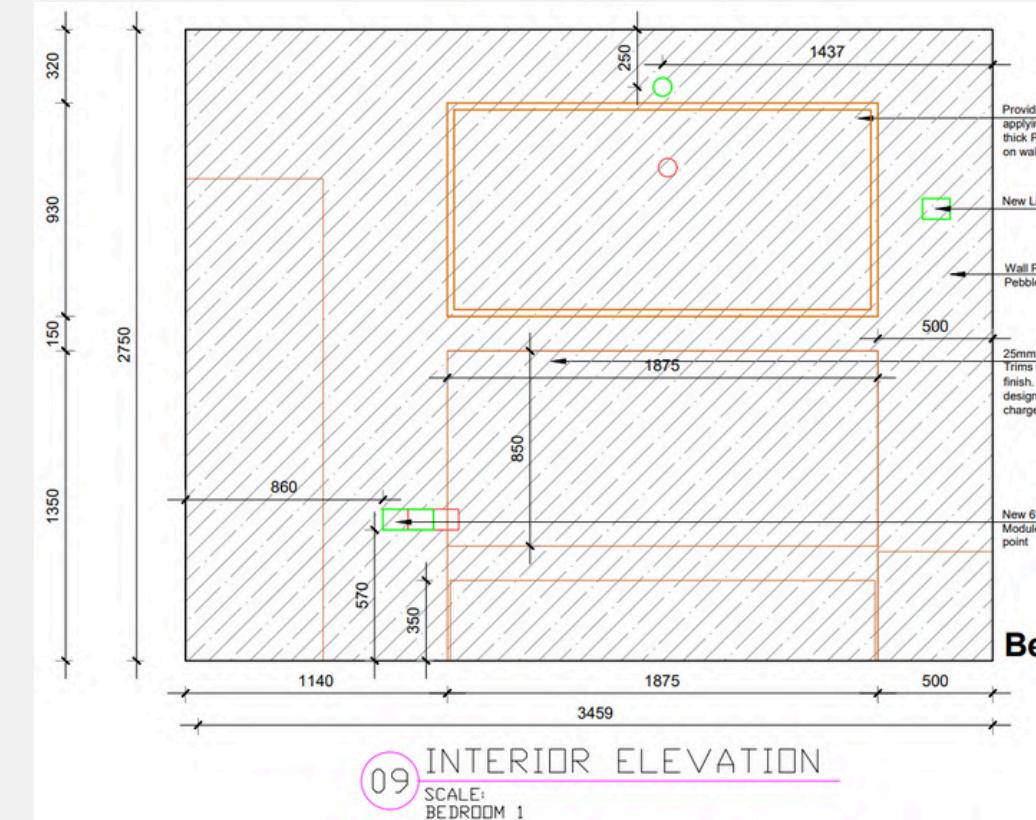

**Bedroom 1**





**Master Bedroom**

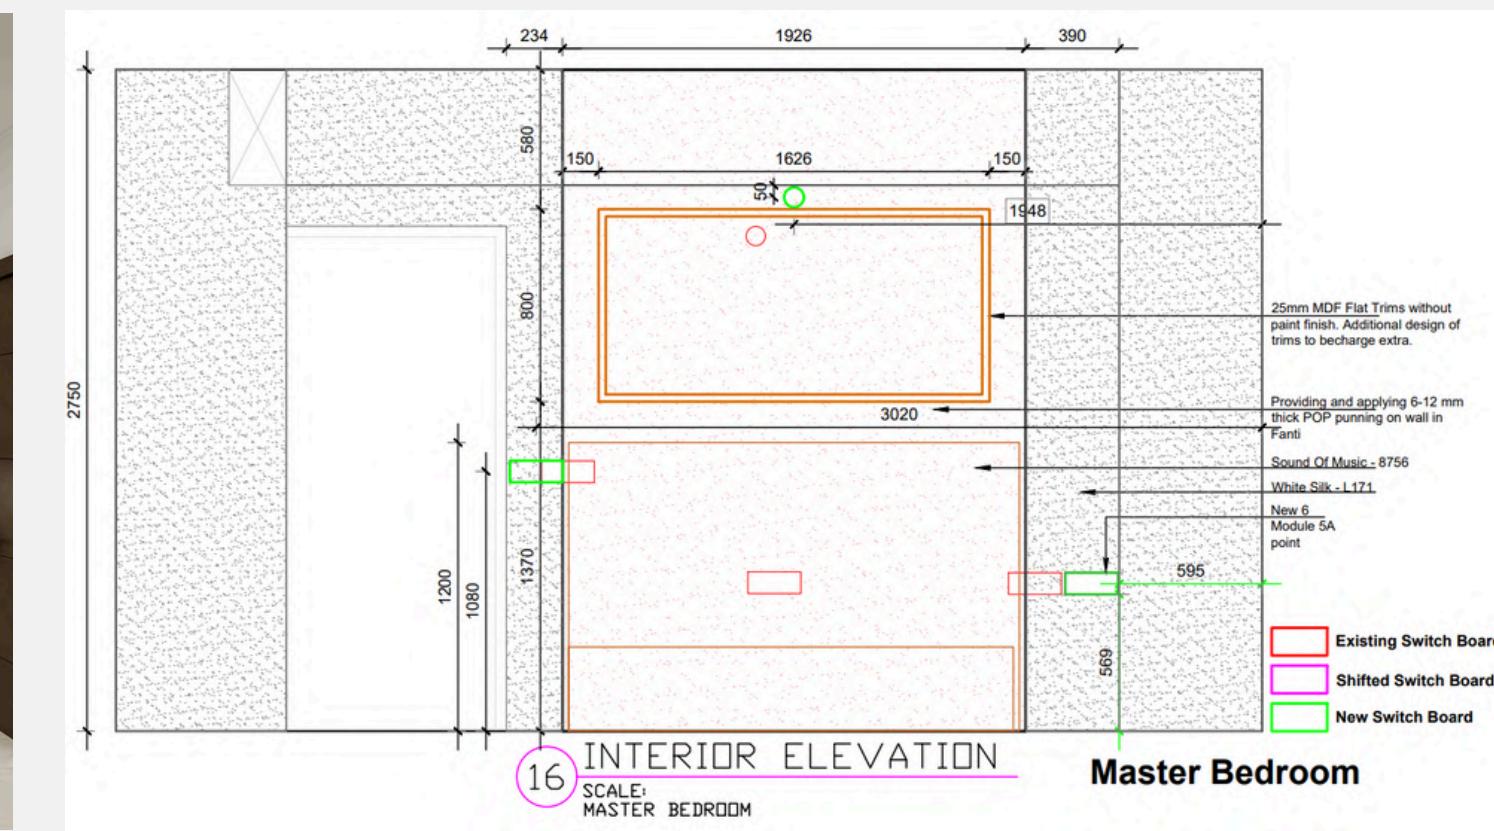

# Kitchen





## Shutter Finish - Gloss Membrane Carcass Finish - White Laminate Edge Profile Handles & Knobs for lofts

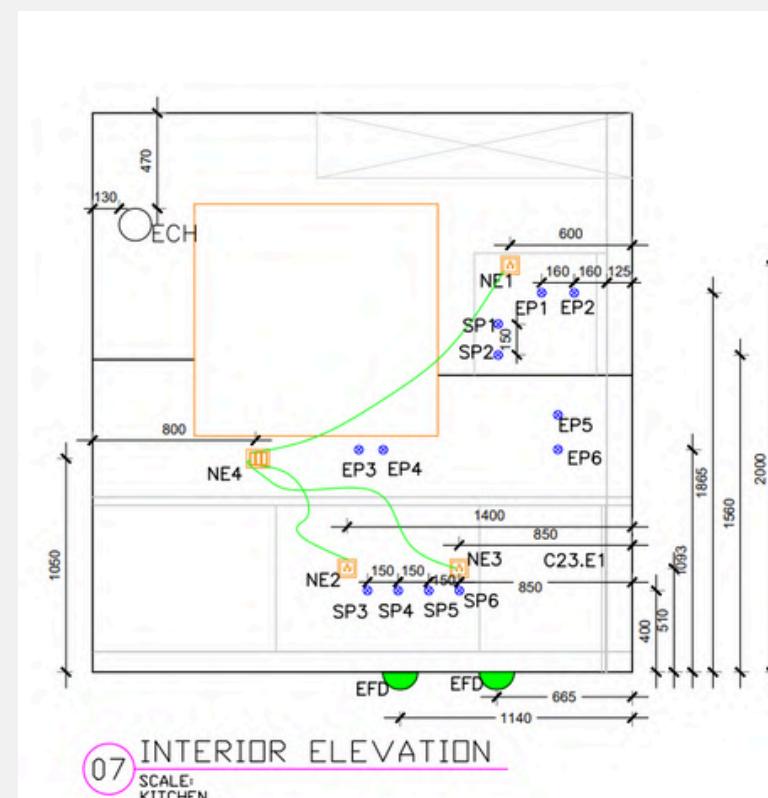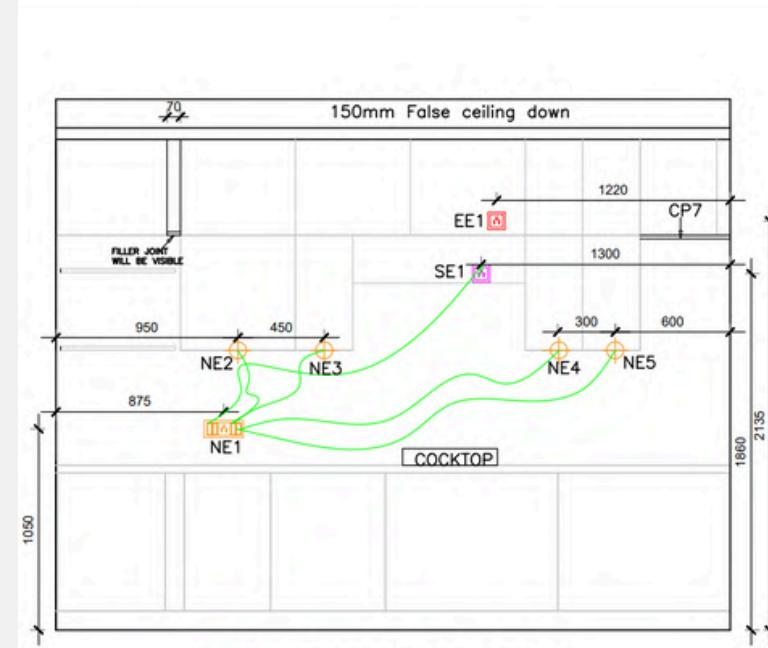



S.No	Code	Description
	NE1	New electrical point for chimney & Mixi grinder
	EE1	Existing Electrical point Will be shifted to SE1
	NE2	New Electrical point for light
	NE3	New Electrical point for light
	NE4	New Electrical point for light
	NE5	New Electrical point for light

**NOTE:** Wall Skirting to be removed behind the KNW cabinets


- Existing Plumbing point (EP)
- New Plumbing point (NP)
- Shifted Plumbing point (SP)
- Existing electrical point (EE)
- New electrical point (NE)
- Shifted electrical point (SE)

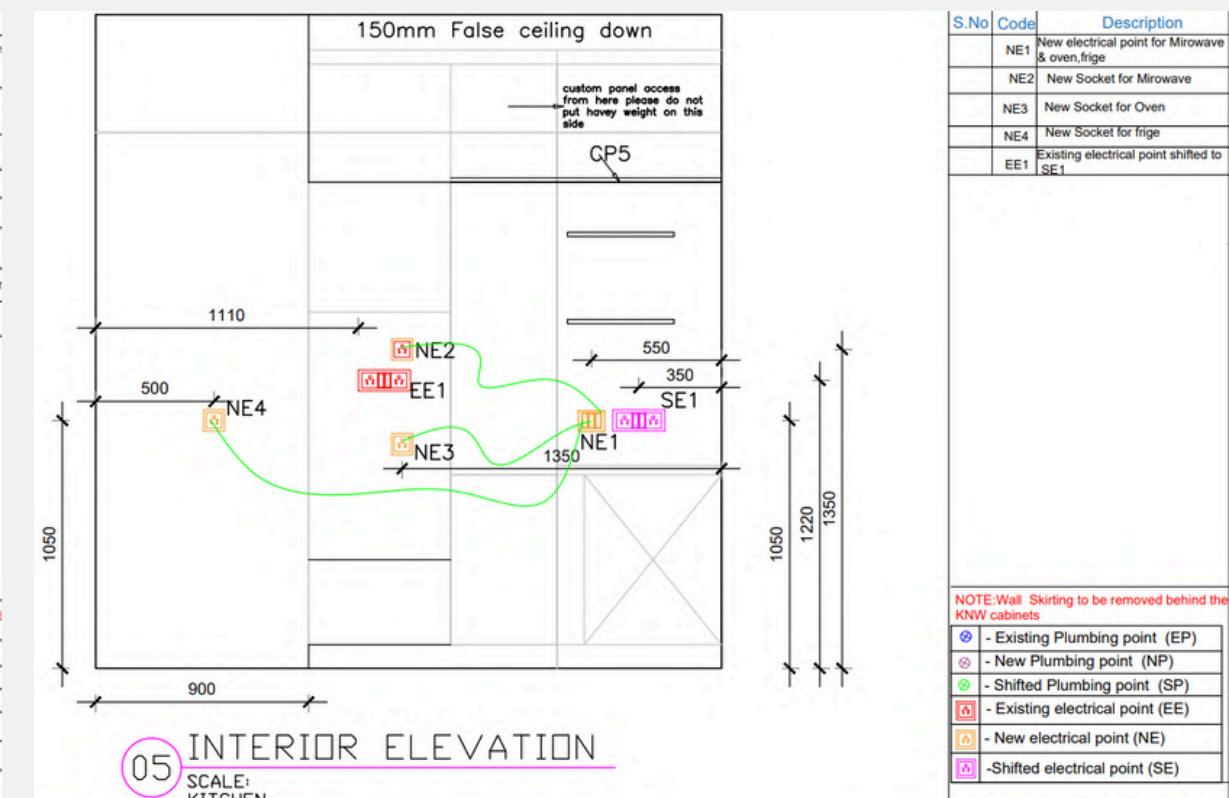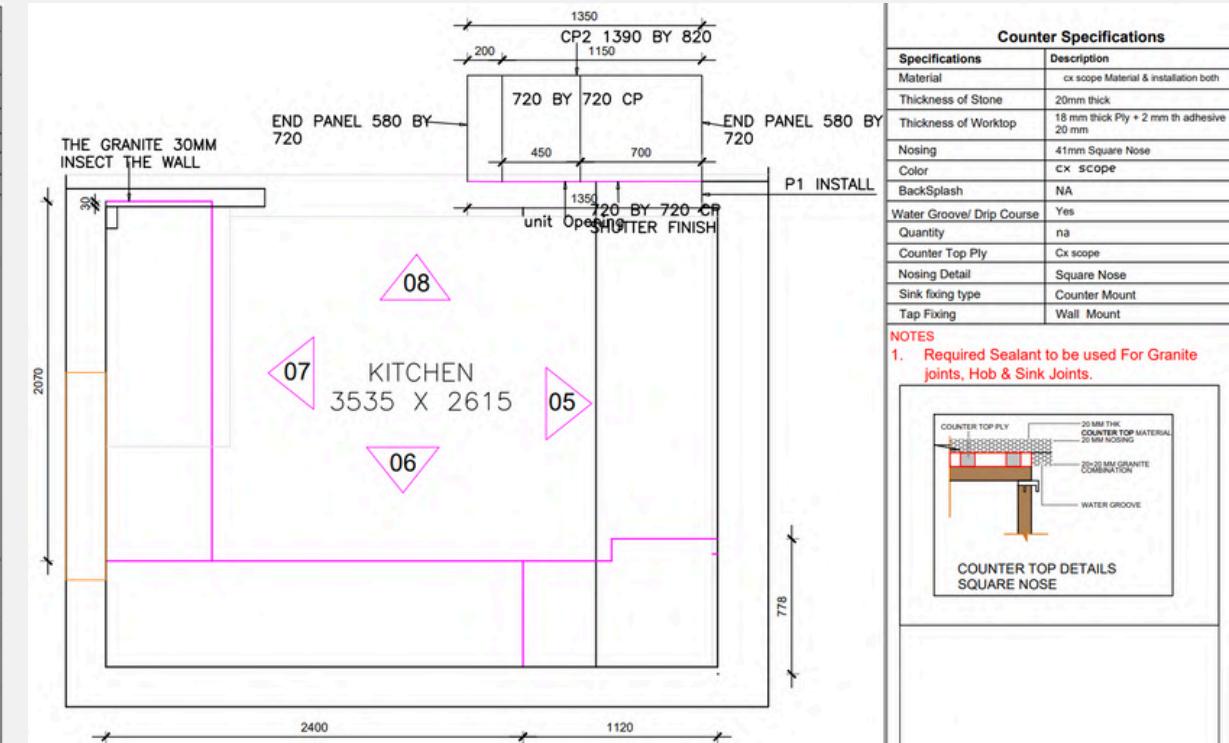


## Living & Dining

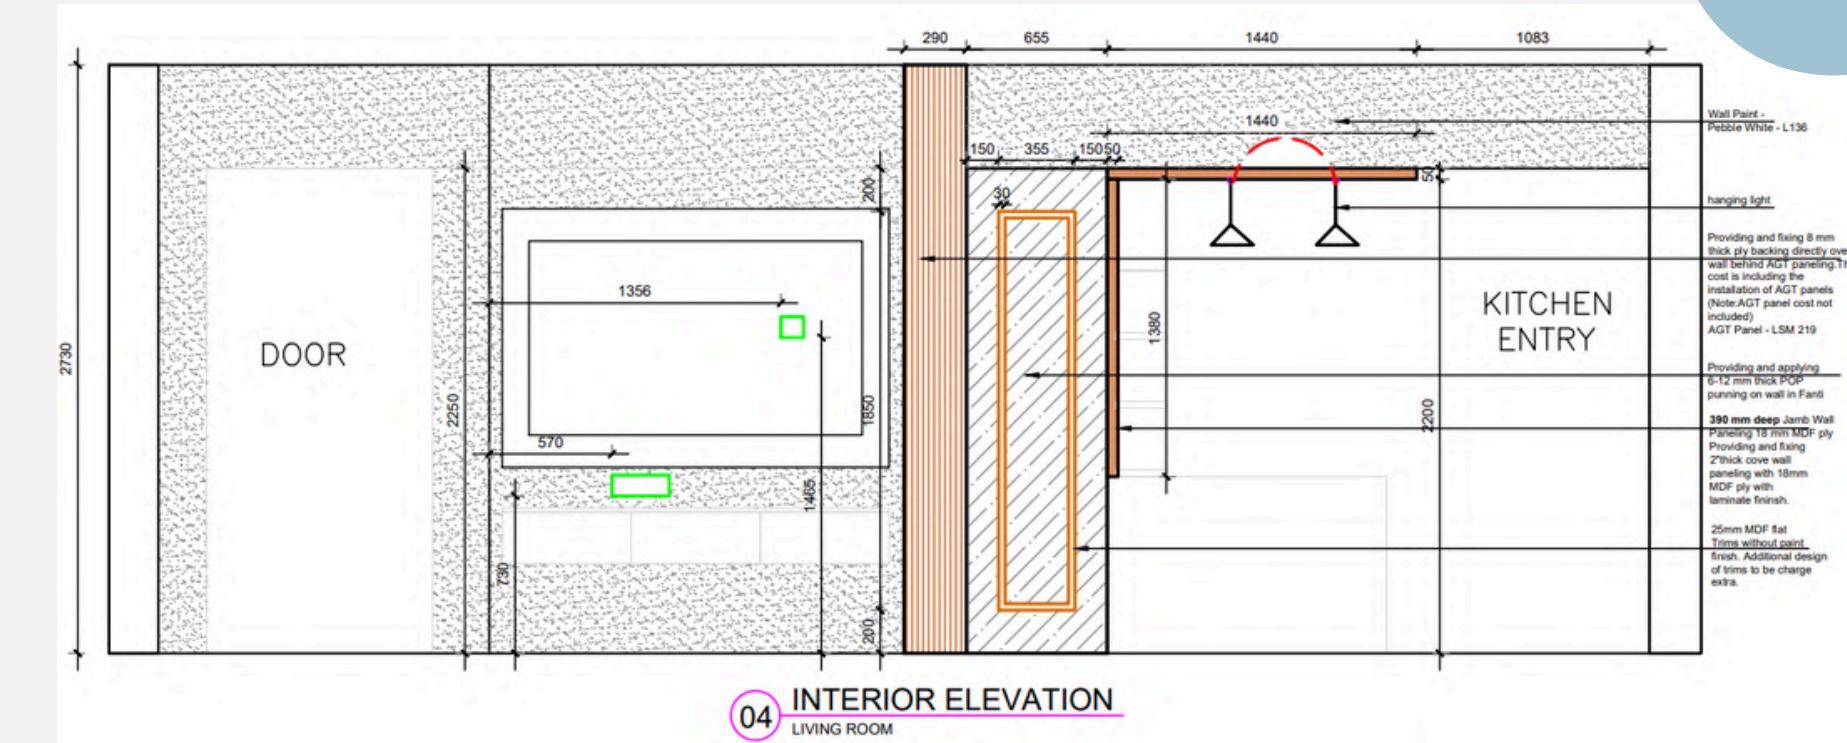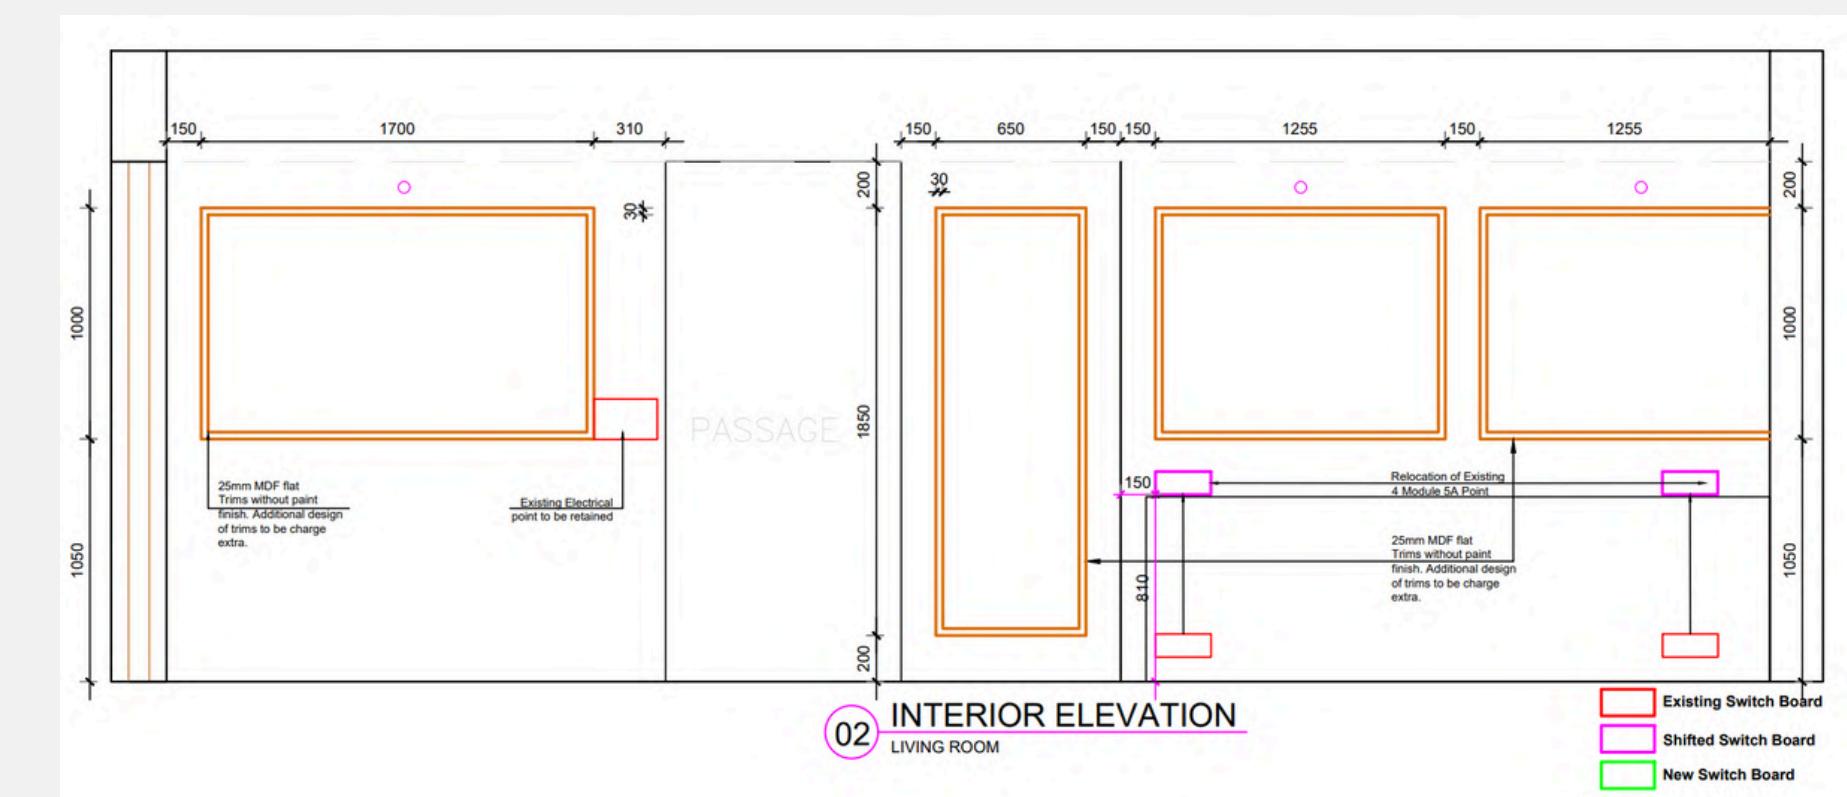

## Other Areas

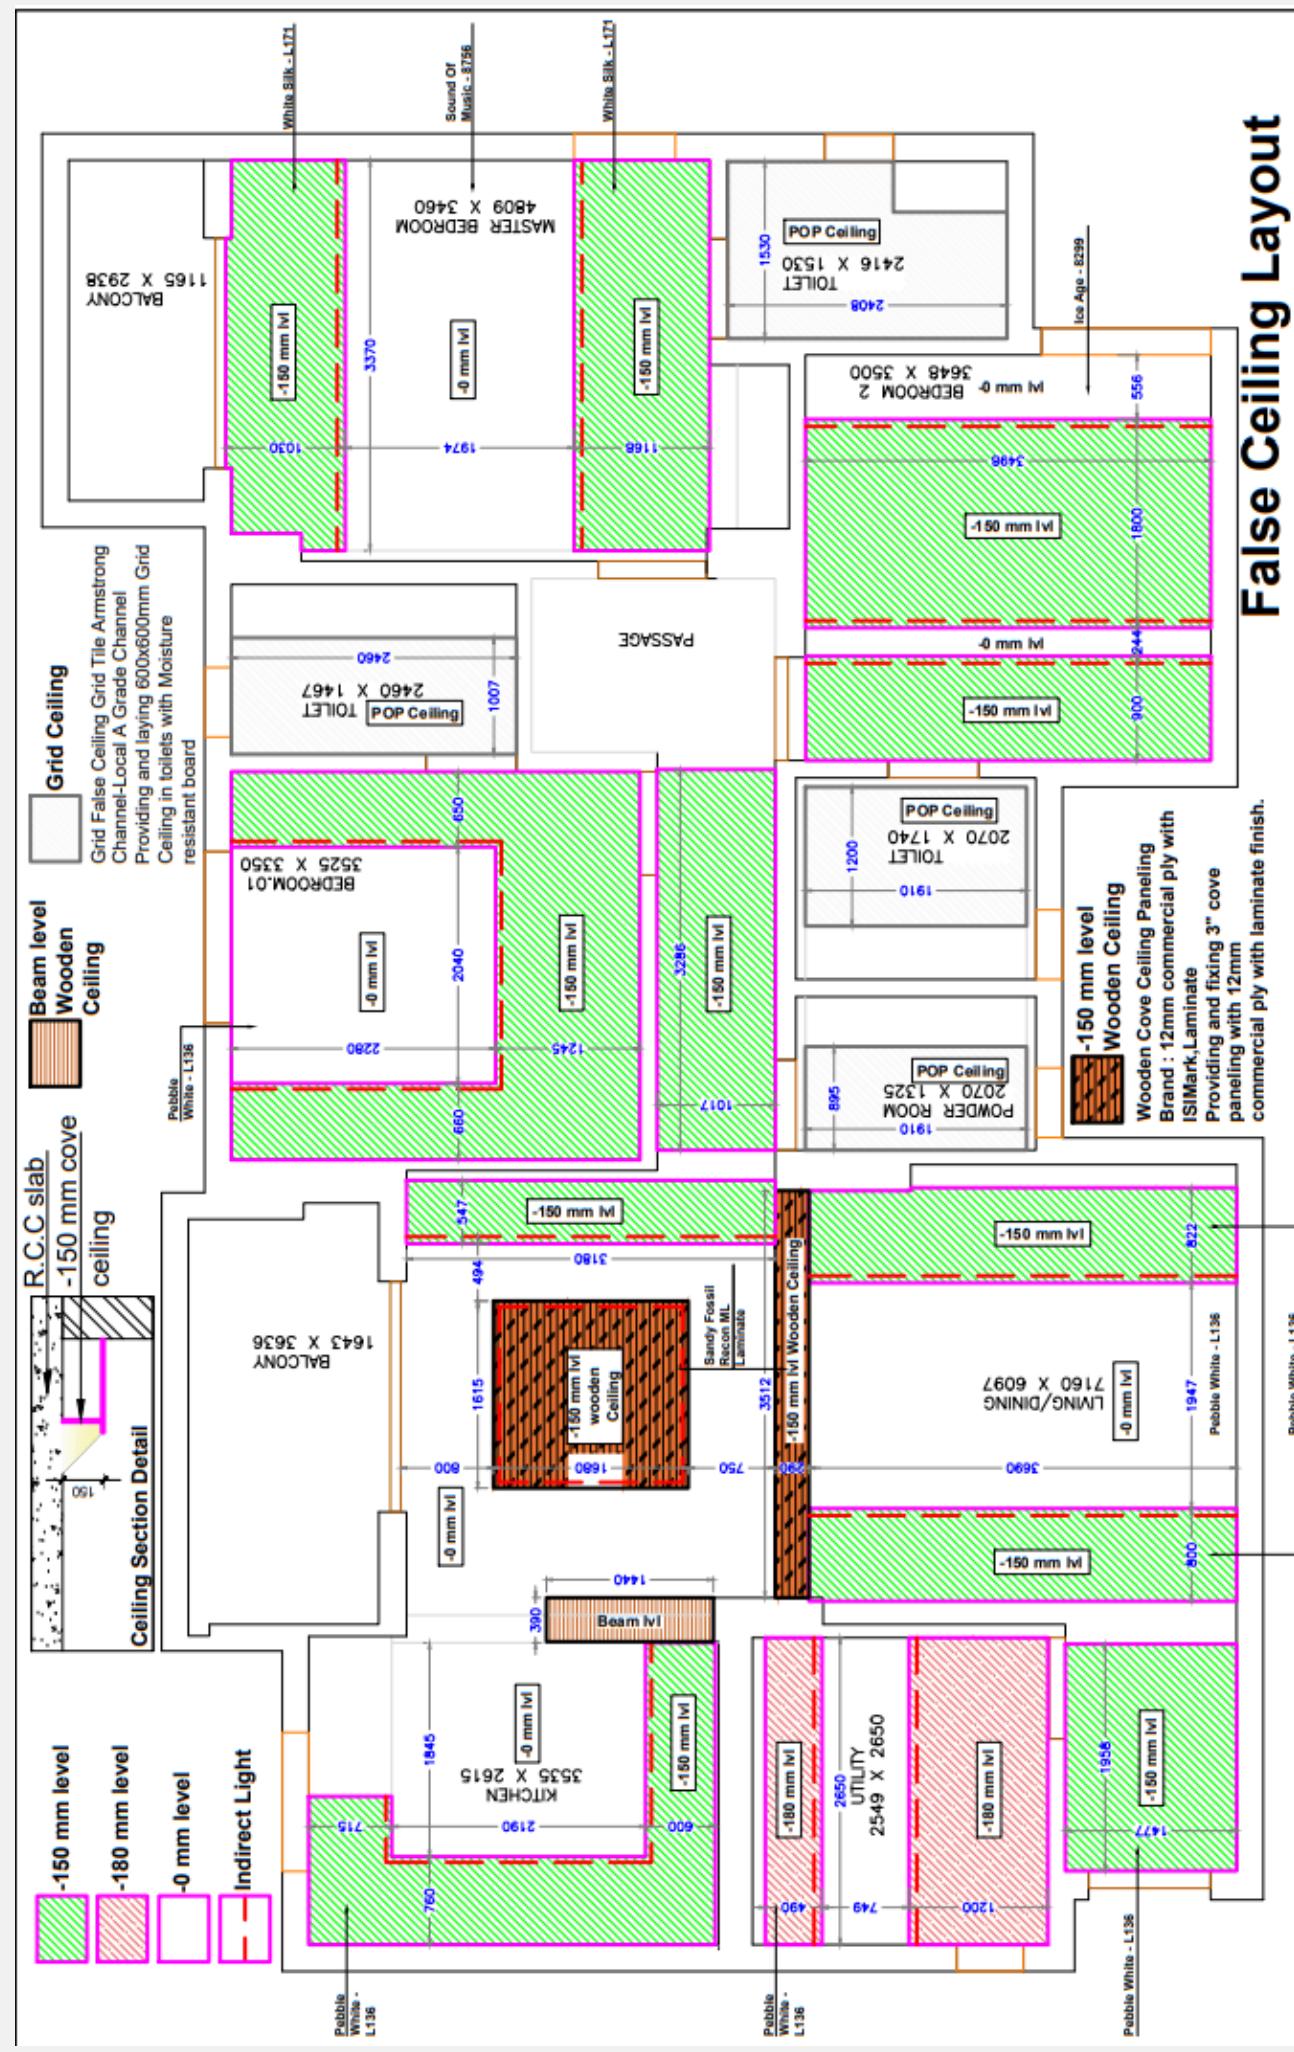

False Ceiling Layout

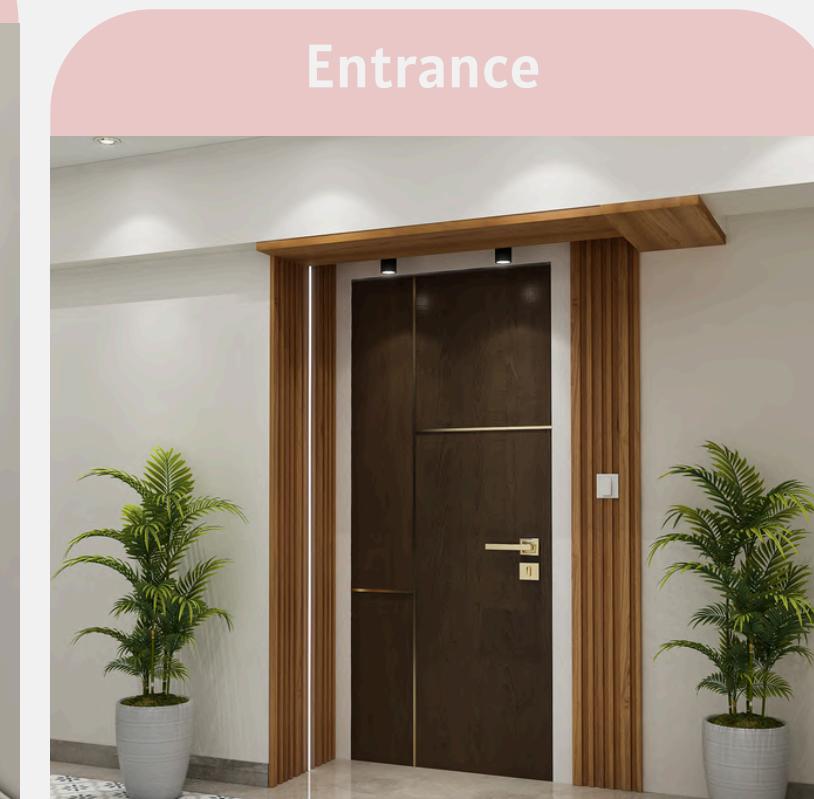

# Full Home Residential Project - 2

**Location - Flat no. 401, 7II-A shanti nagar, Durgapura, Jaipur .**

**Area –4 BHK (1400 sq.ft.)**

**This is a builder apartment in a peaceful society of Jaipur.**

**Area comprises of 4 spacious Bedrooms along with a welcoming Living area attached to an Open Kitchen.**

**Client, being an independent woman with a super busy schedule and a responsible elder daughter at the same time, required a cozy & soothing space in Jaipur for her family and relatives to have gatherings and get-togethers too.**



## Scope -

- Modular Kitchen
- Modular Wardrobe & Storages
- Furniture
- Civil work
- Services





## Living Area


### Living Area

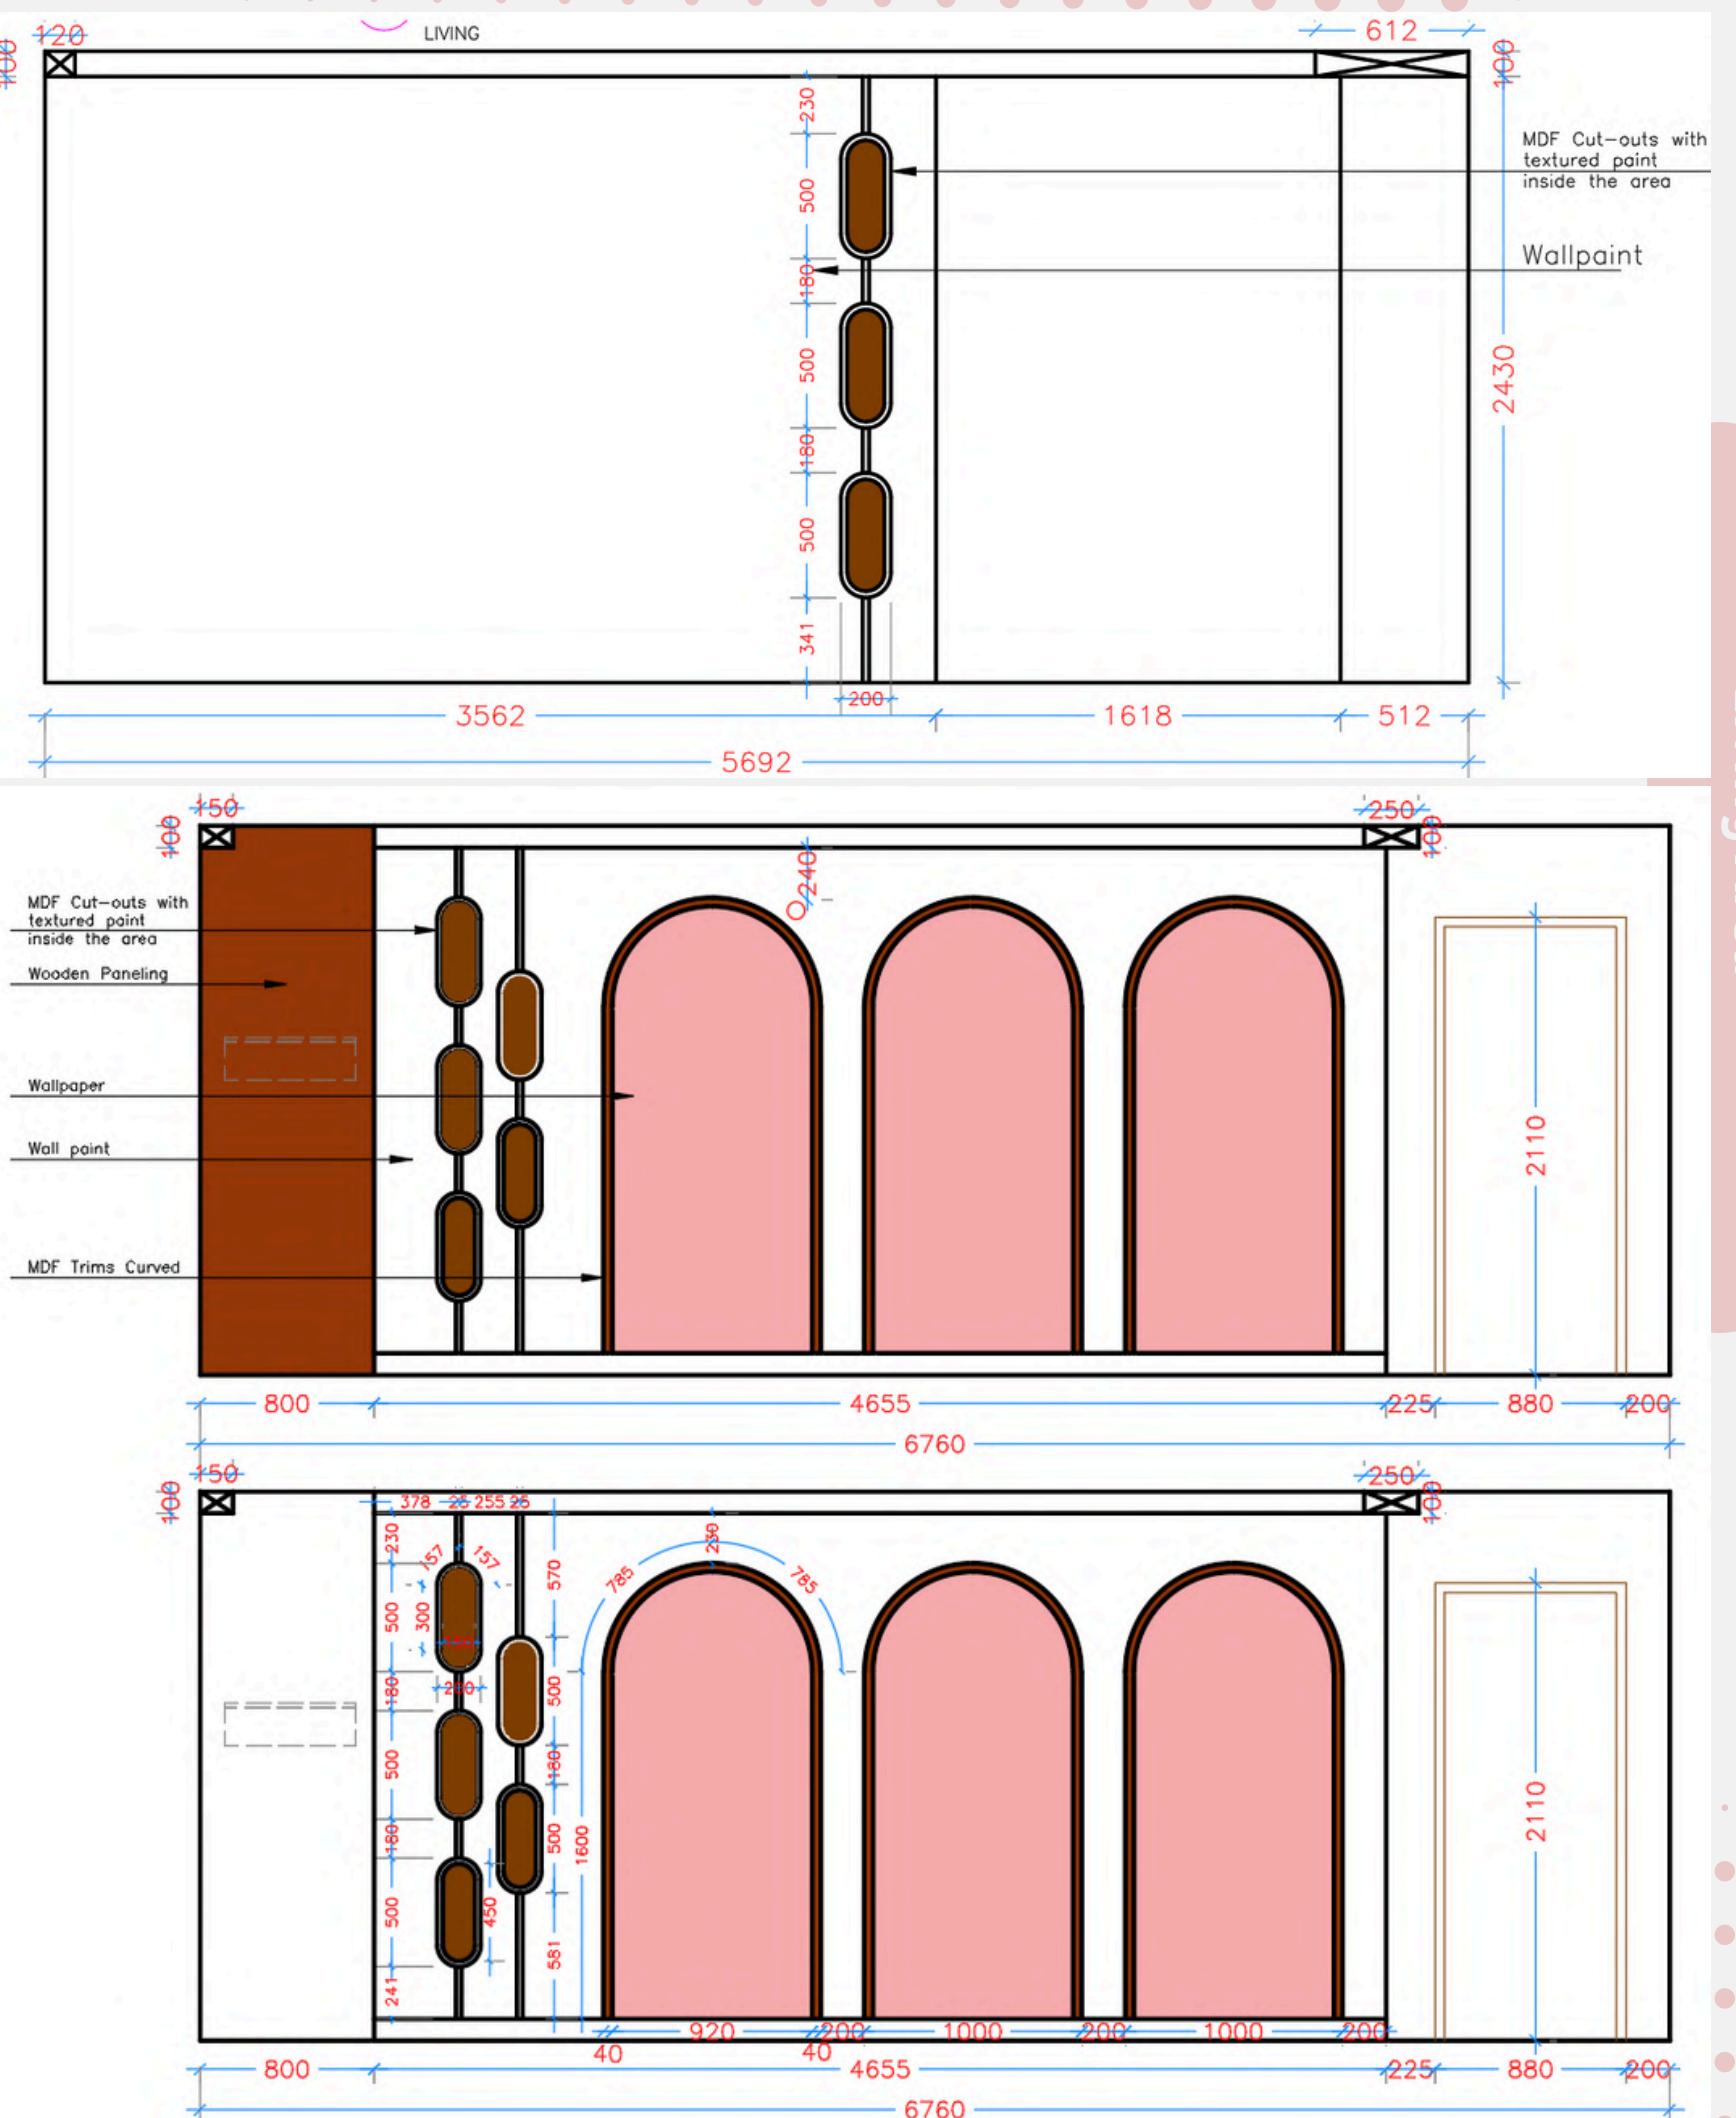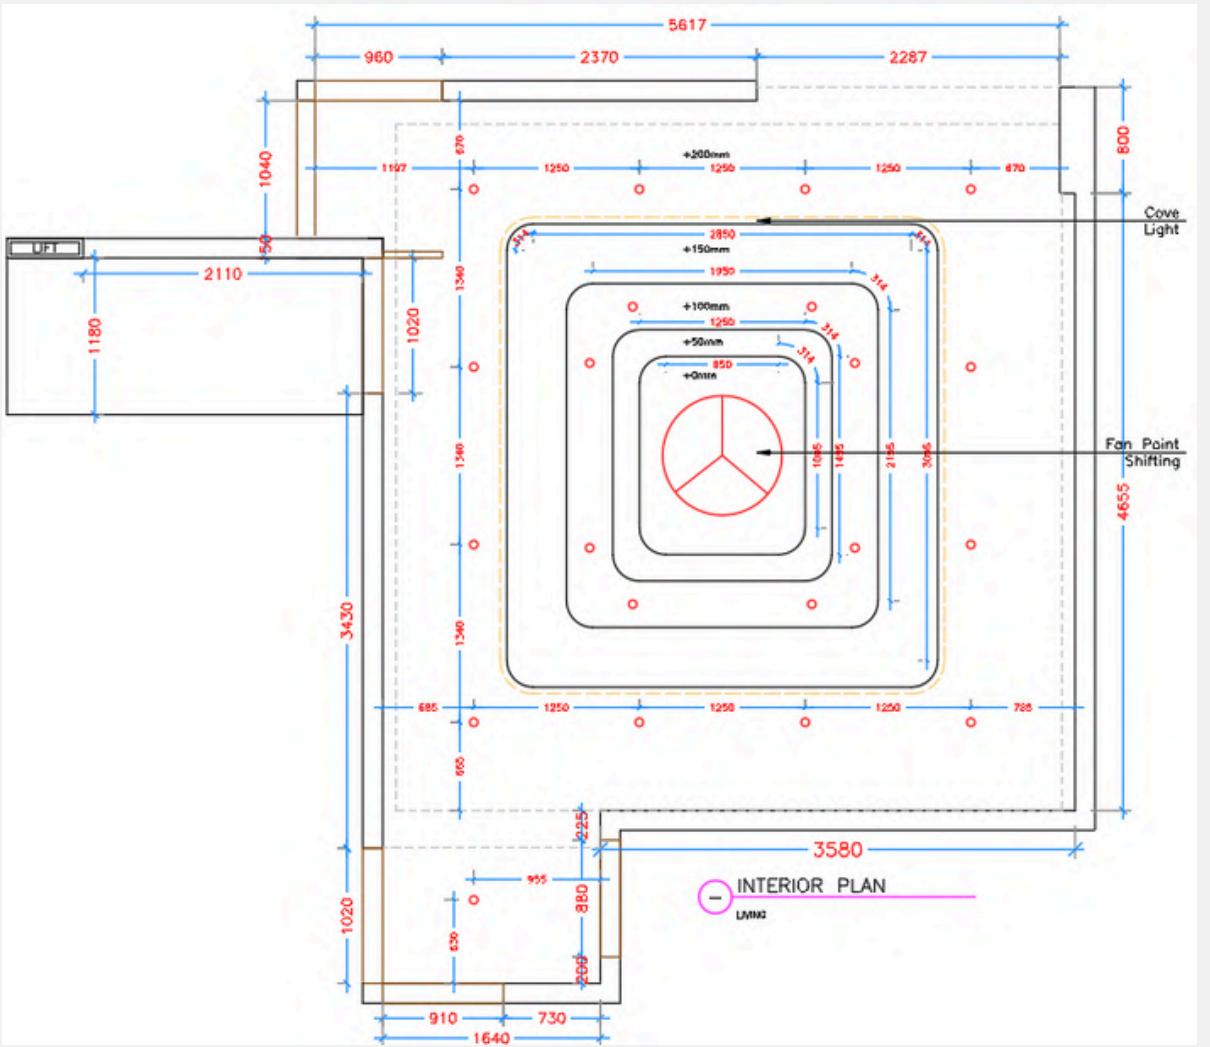



## Living Area

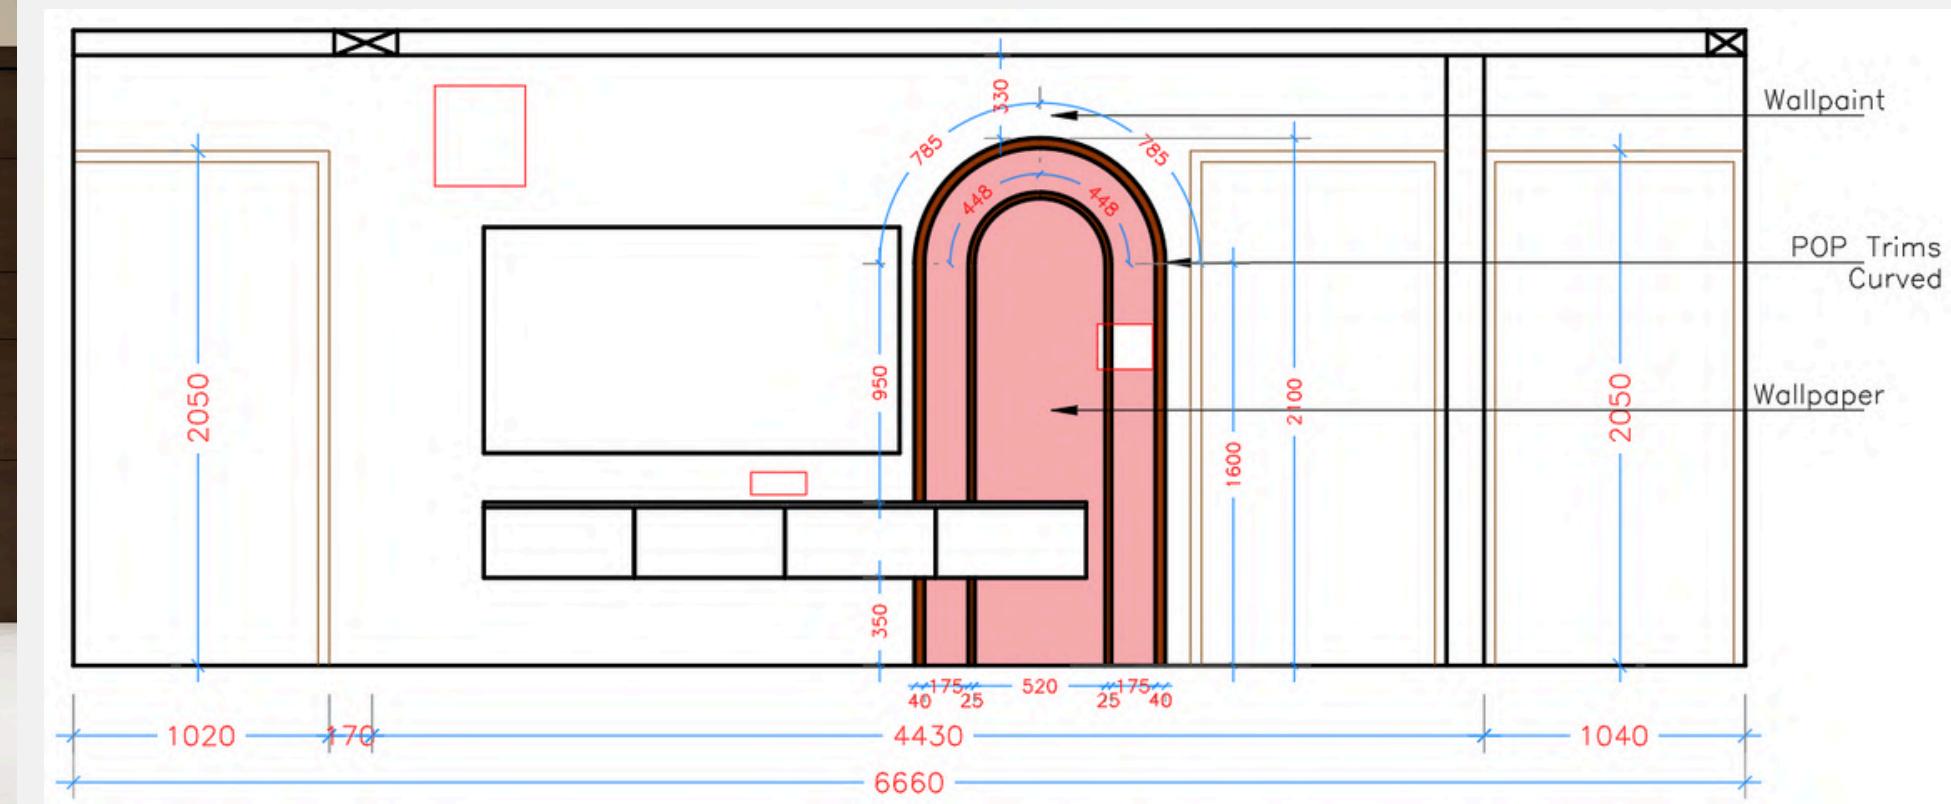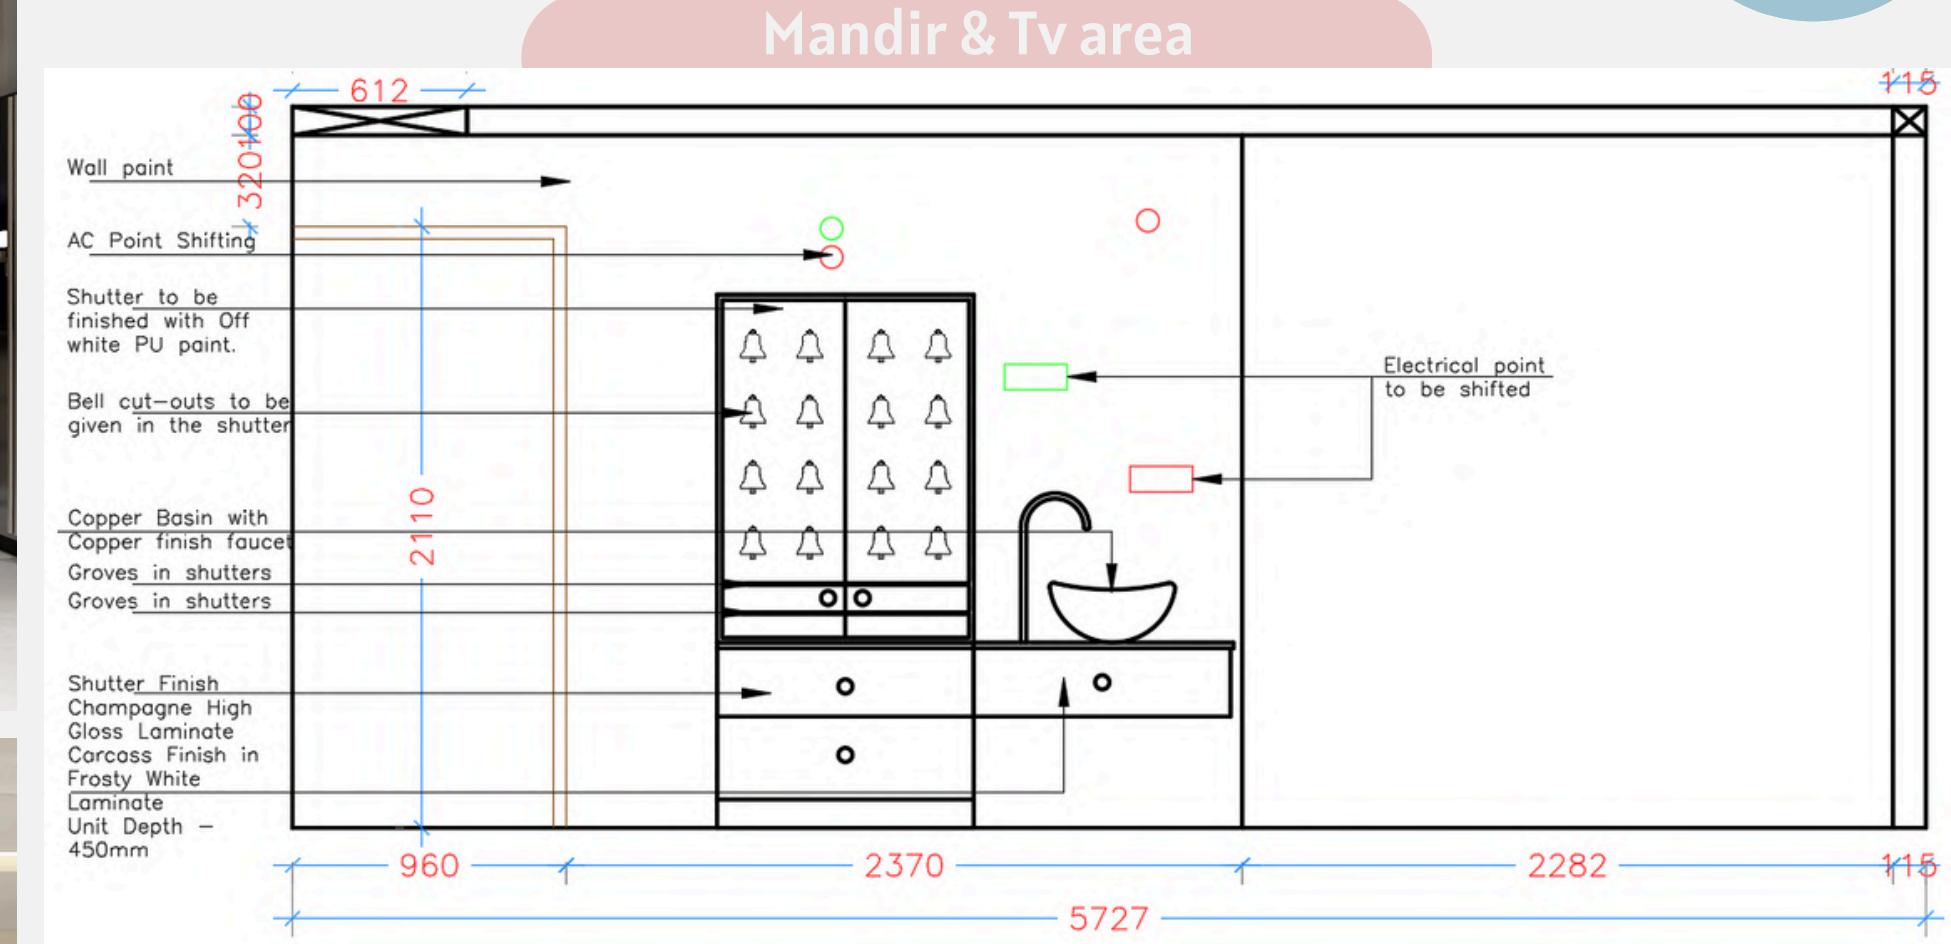



## Bedroom

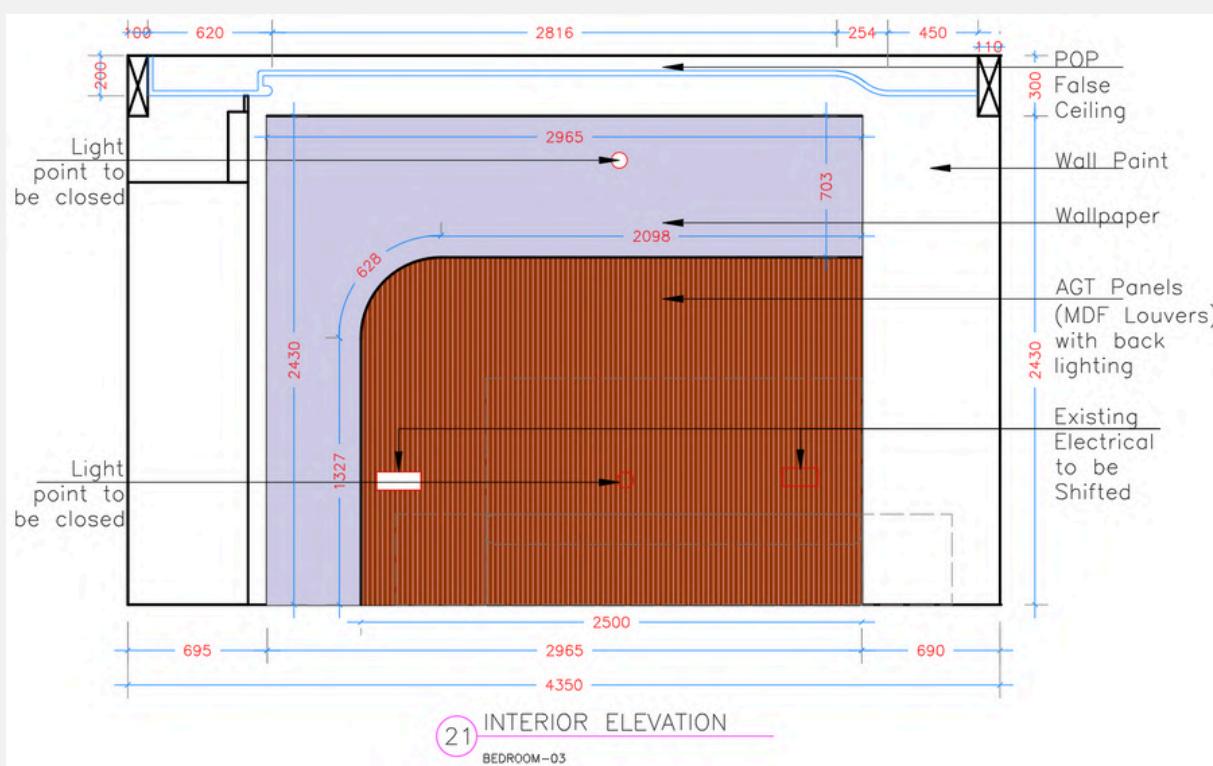

# BEDROOM

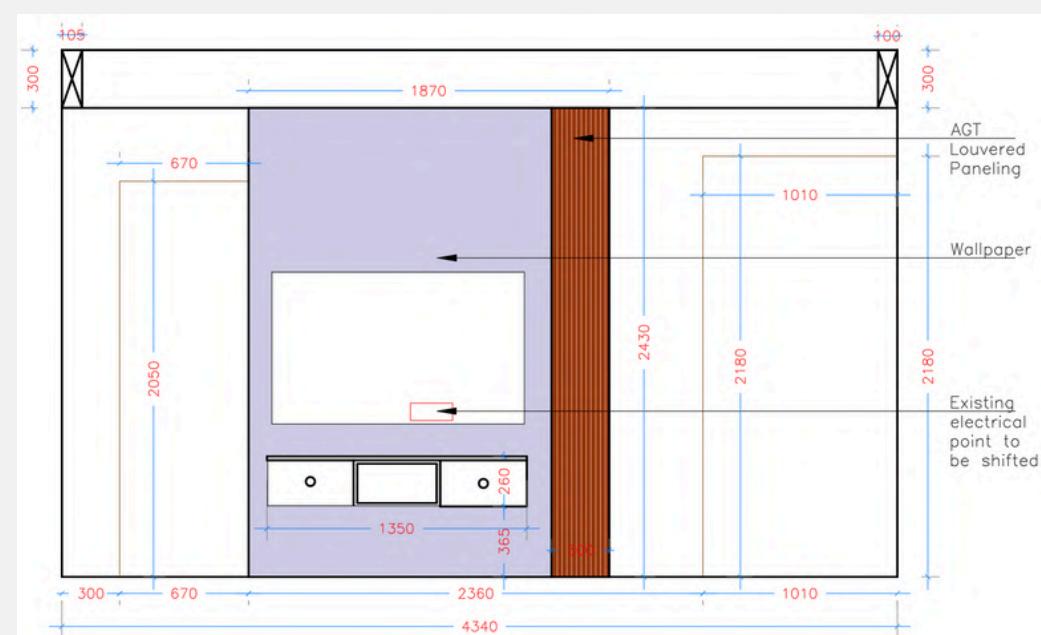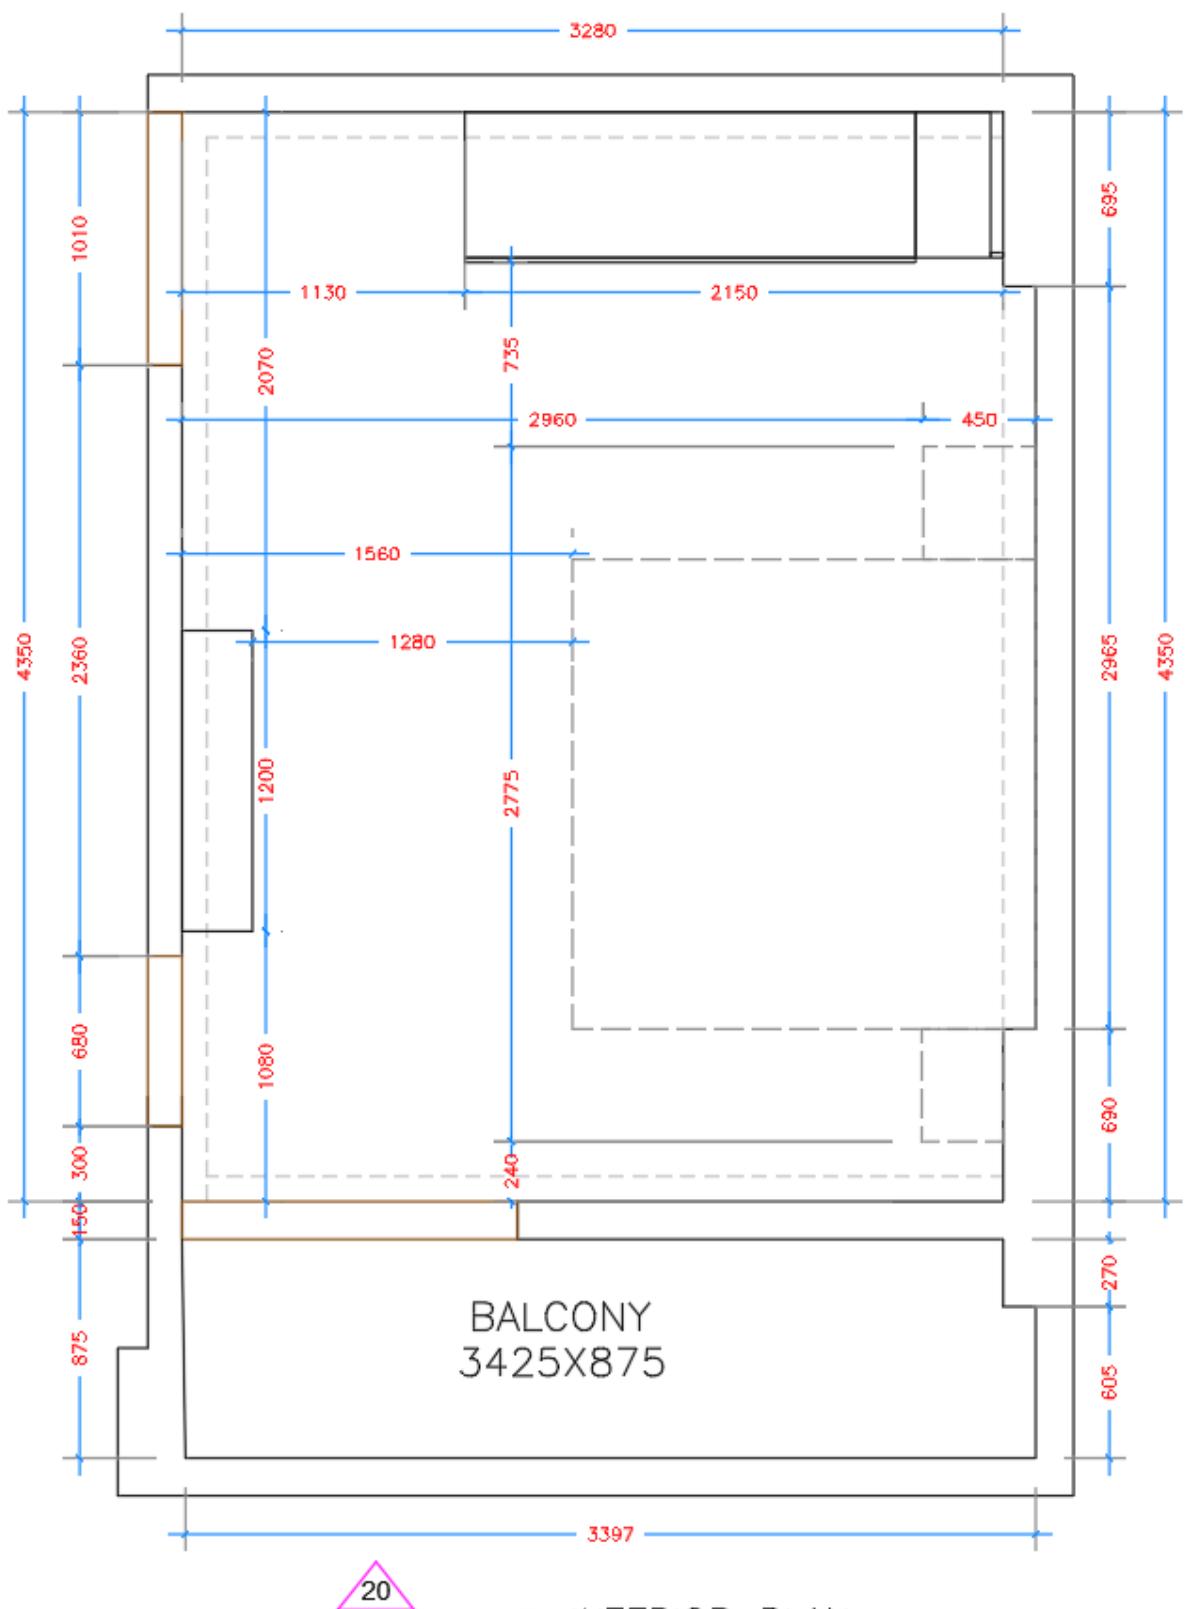

## Bedroom

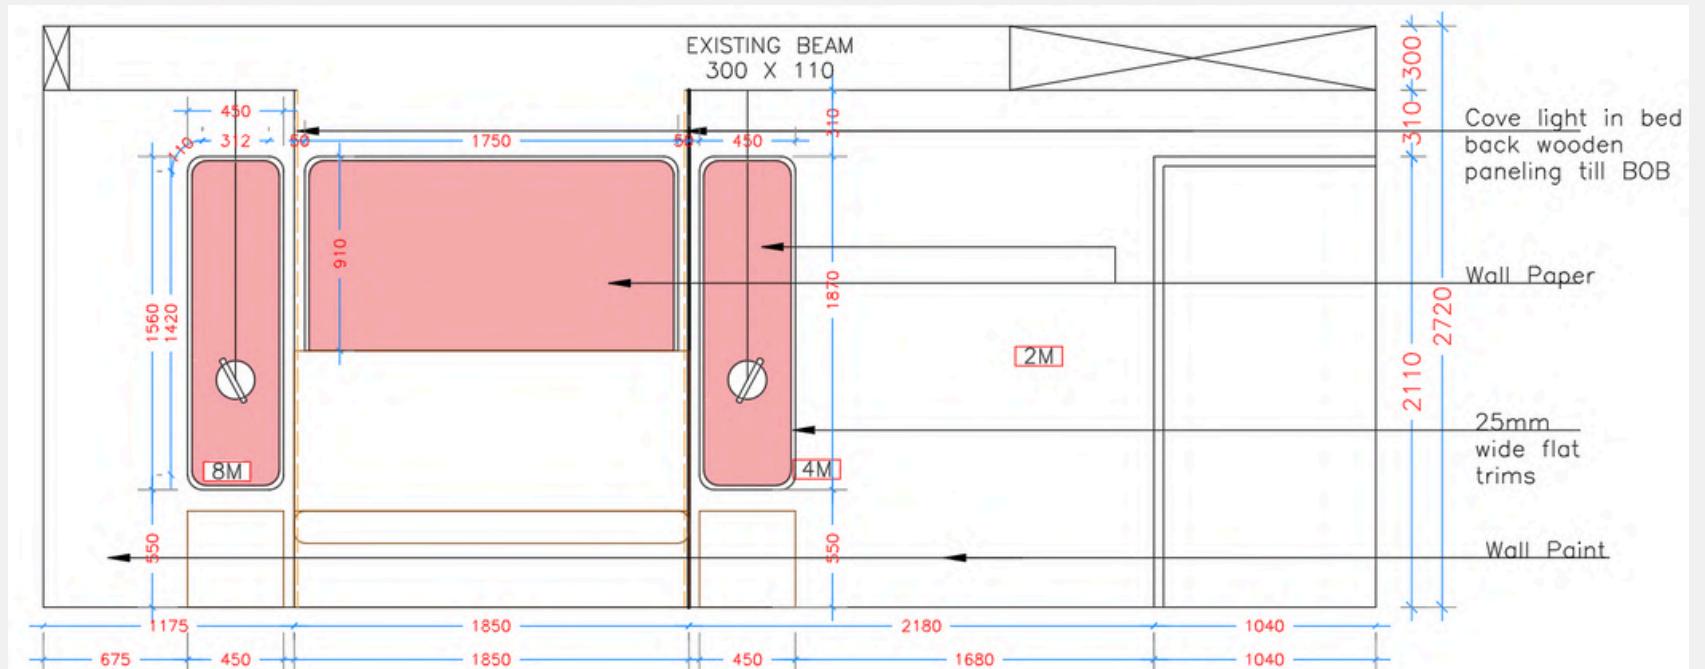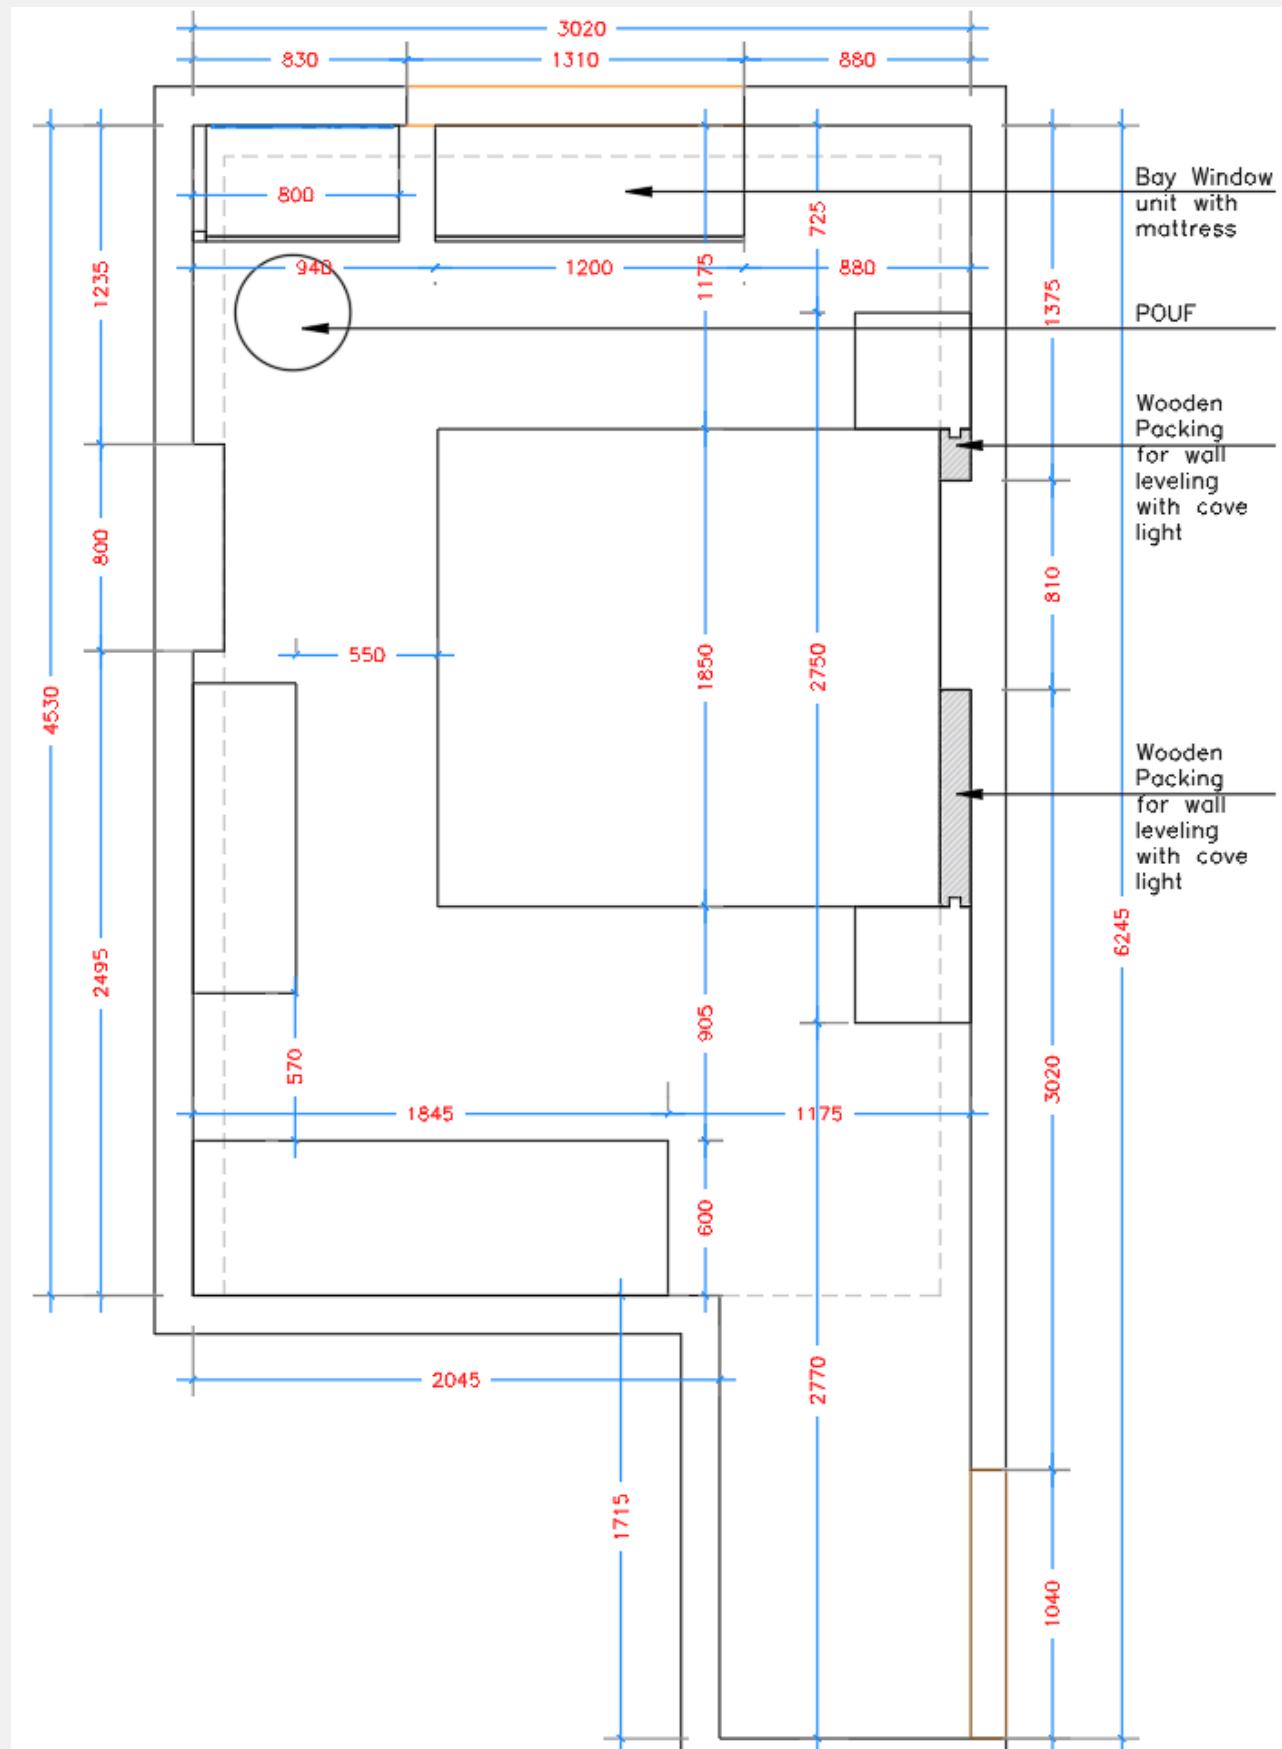

## Bedroom




BEDROOMS



## Aaditya Bath

### Showroom

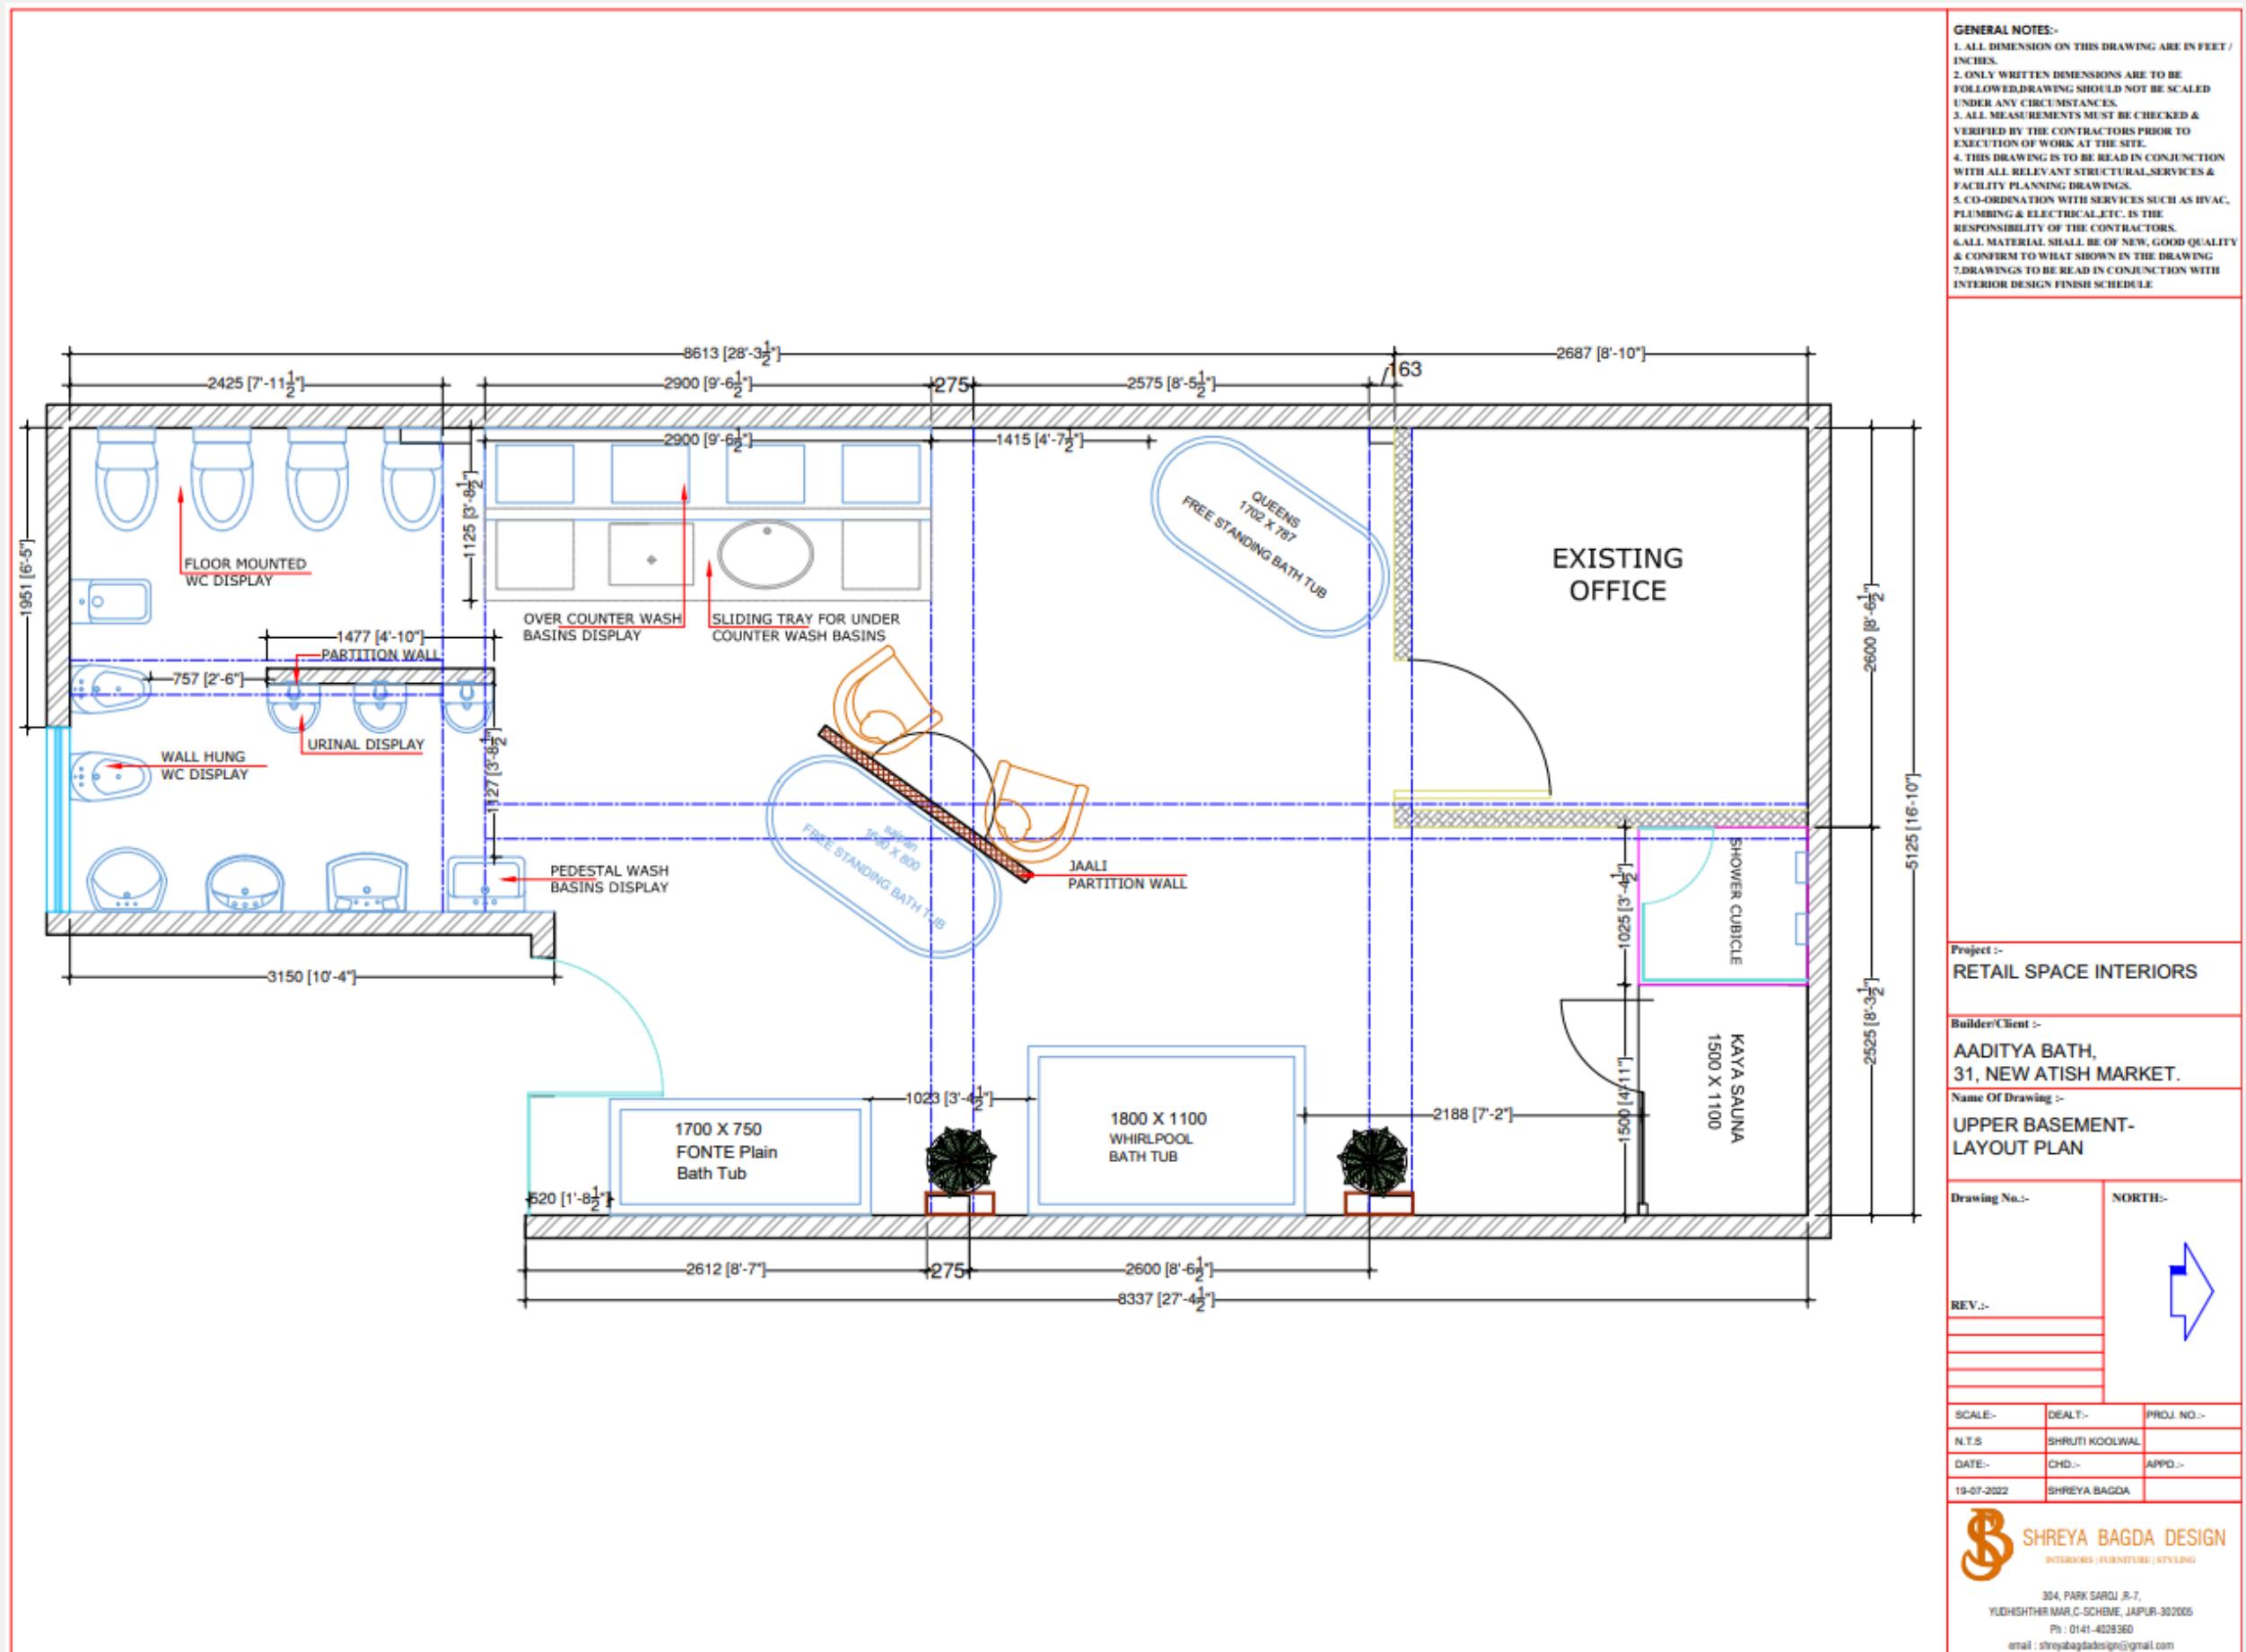

**Location** - 31, New Atish Market, Mansarovar, Jaipur, Rajasthan.

**Area** - Basement (623 sq.ft.)

This is a Sanitary ware supplier showroom in, Jaipur.

Its basement had to get renewed to give it a look of a soothing spa/sauna-like space.

- Furniture Layout, 3D Model Concept.

Showroom

3D Views



# Satyam House

Location – Vaishali Nagar, Jaipur, Rajasthan.

Area – 4000 sq. ft.

This project is a G+3 Storey House.

- On the ground floor, there is a kitchen and Pooja room joining the drawing room and the double-height living area outside a guest room and a parent's bedroom.
- On the first floor there are 3 bedrooms including the master's, daughter's, and son's room.
- On the Second floor they have a bedroom along with a Gym, Office, and a home theatre.
- On the third floor, we could observe a bedroom attached to a Heath & Spa room.
- The lobby area on the floor is to be treated as a Party area for organizing small family get-togethers and also has a small terrace garden.

## Pooja Area








## Home Office




## Bedroom

## Residential

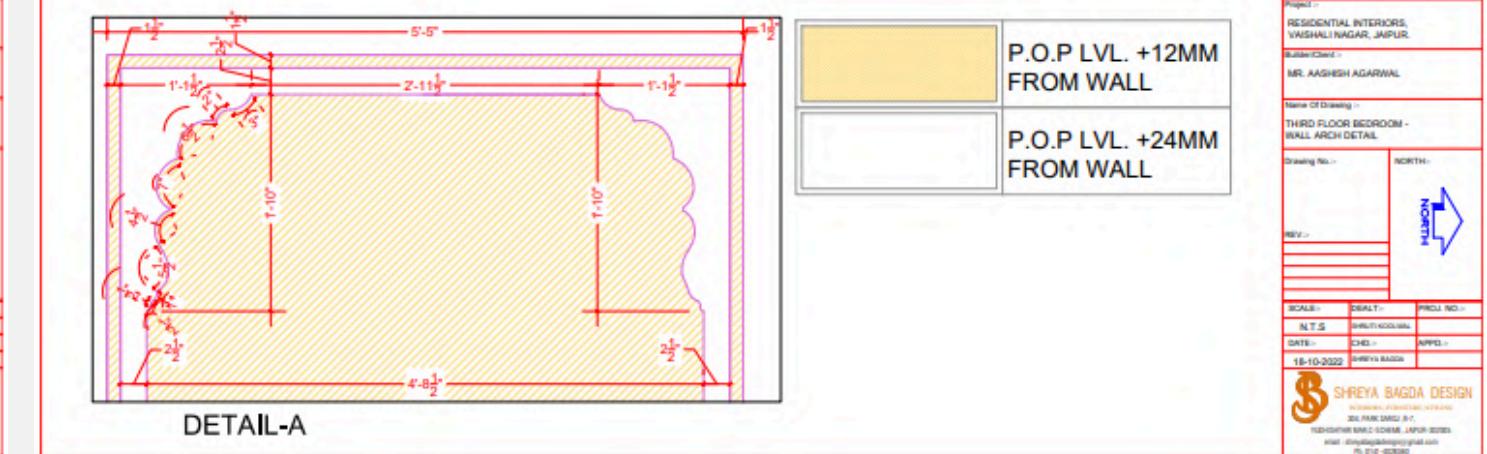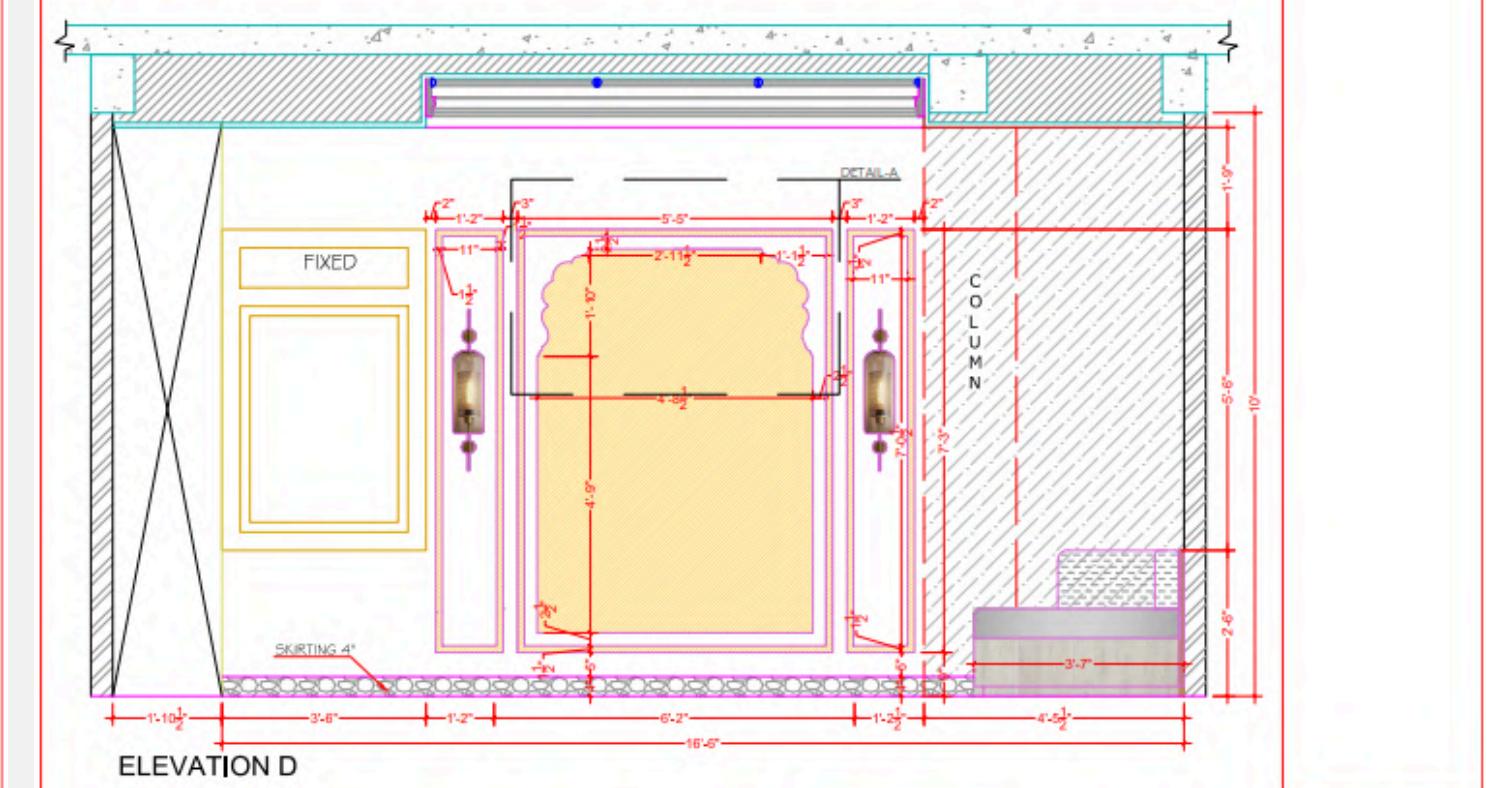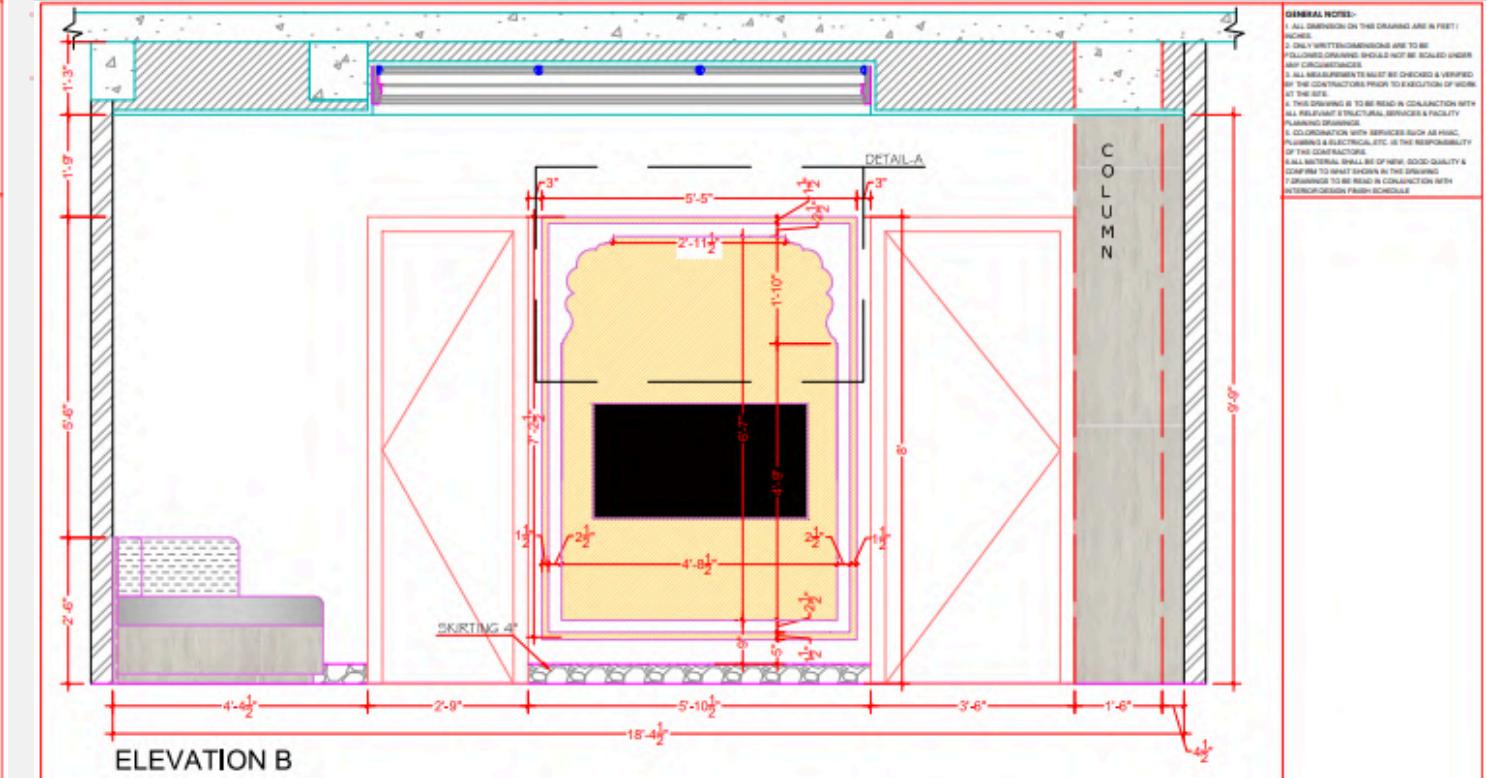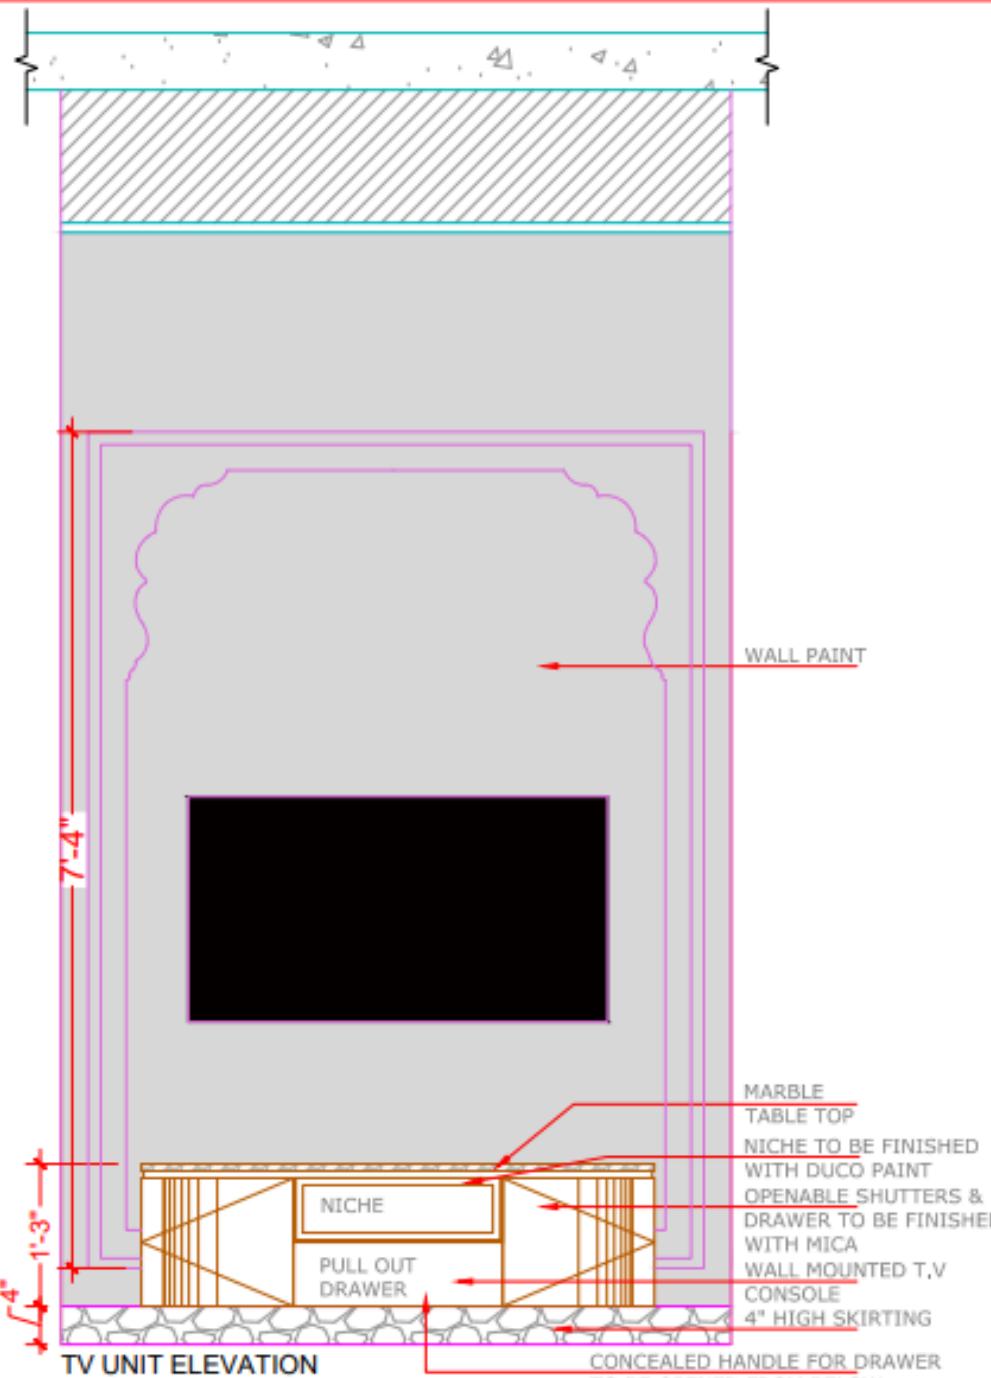


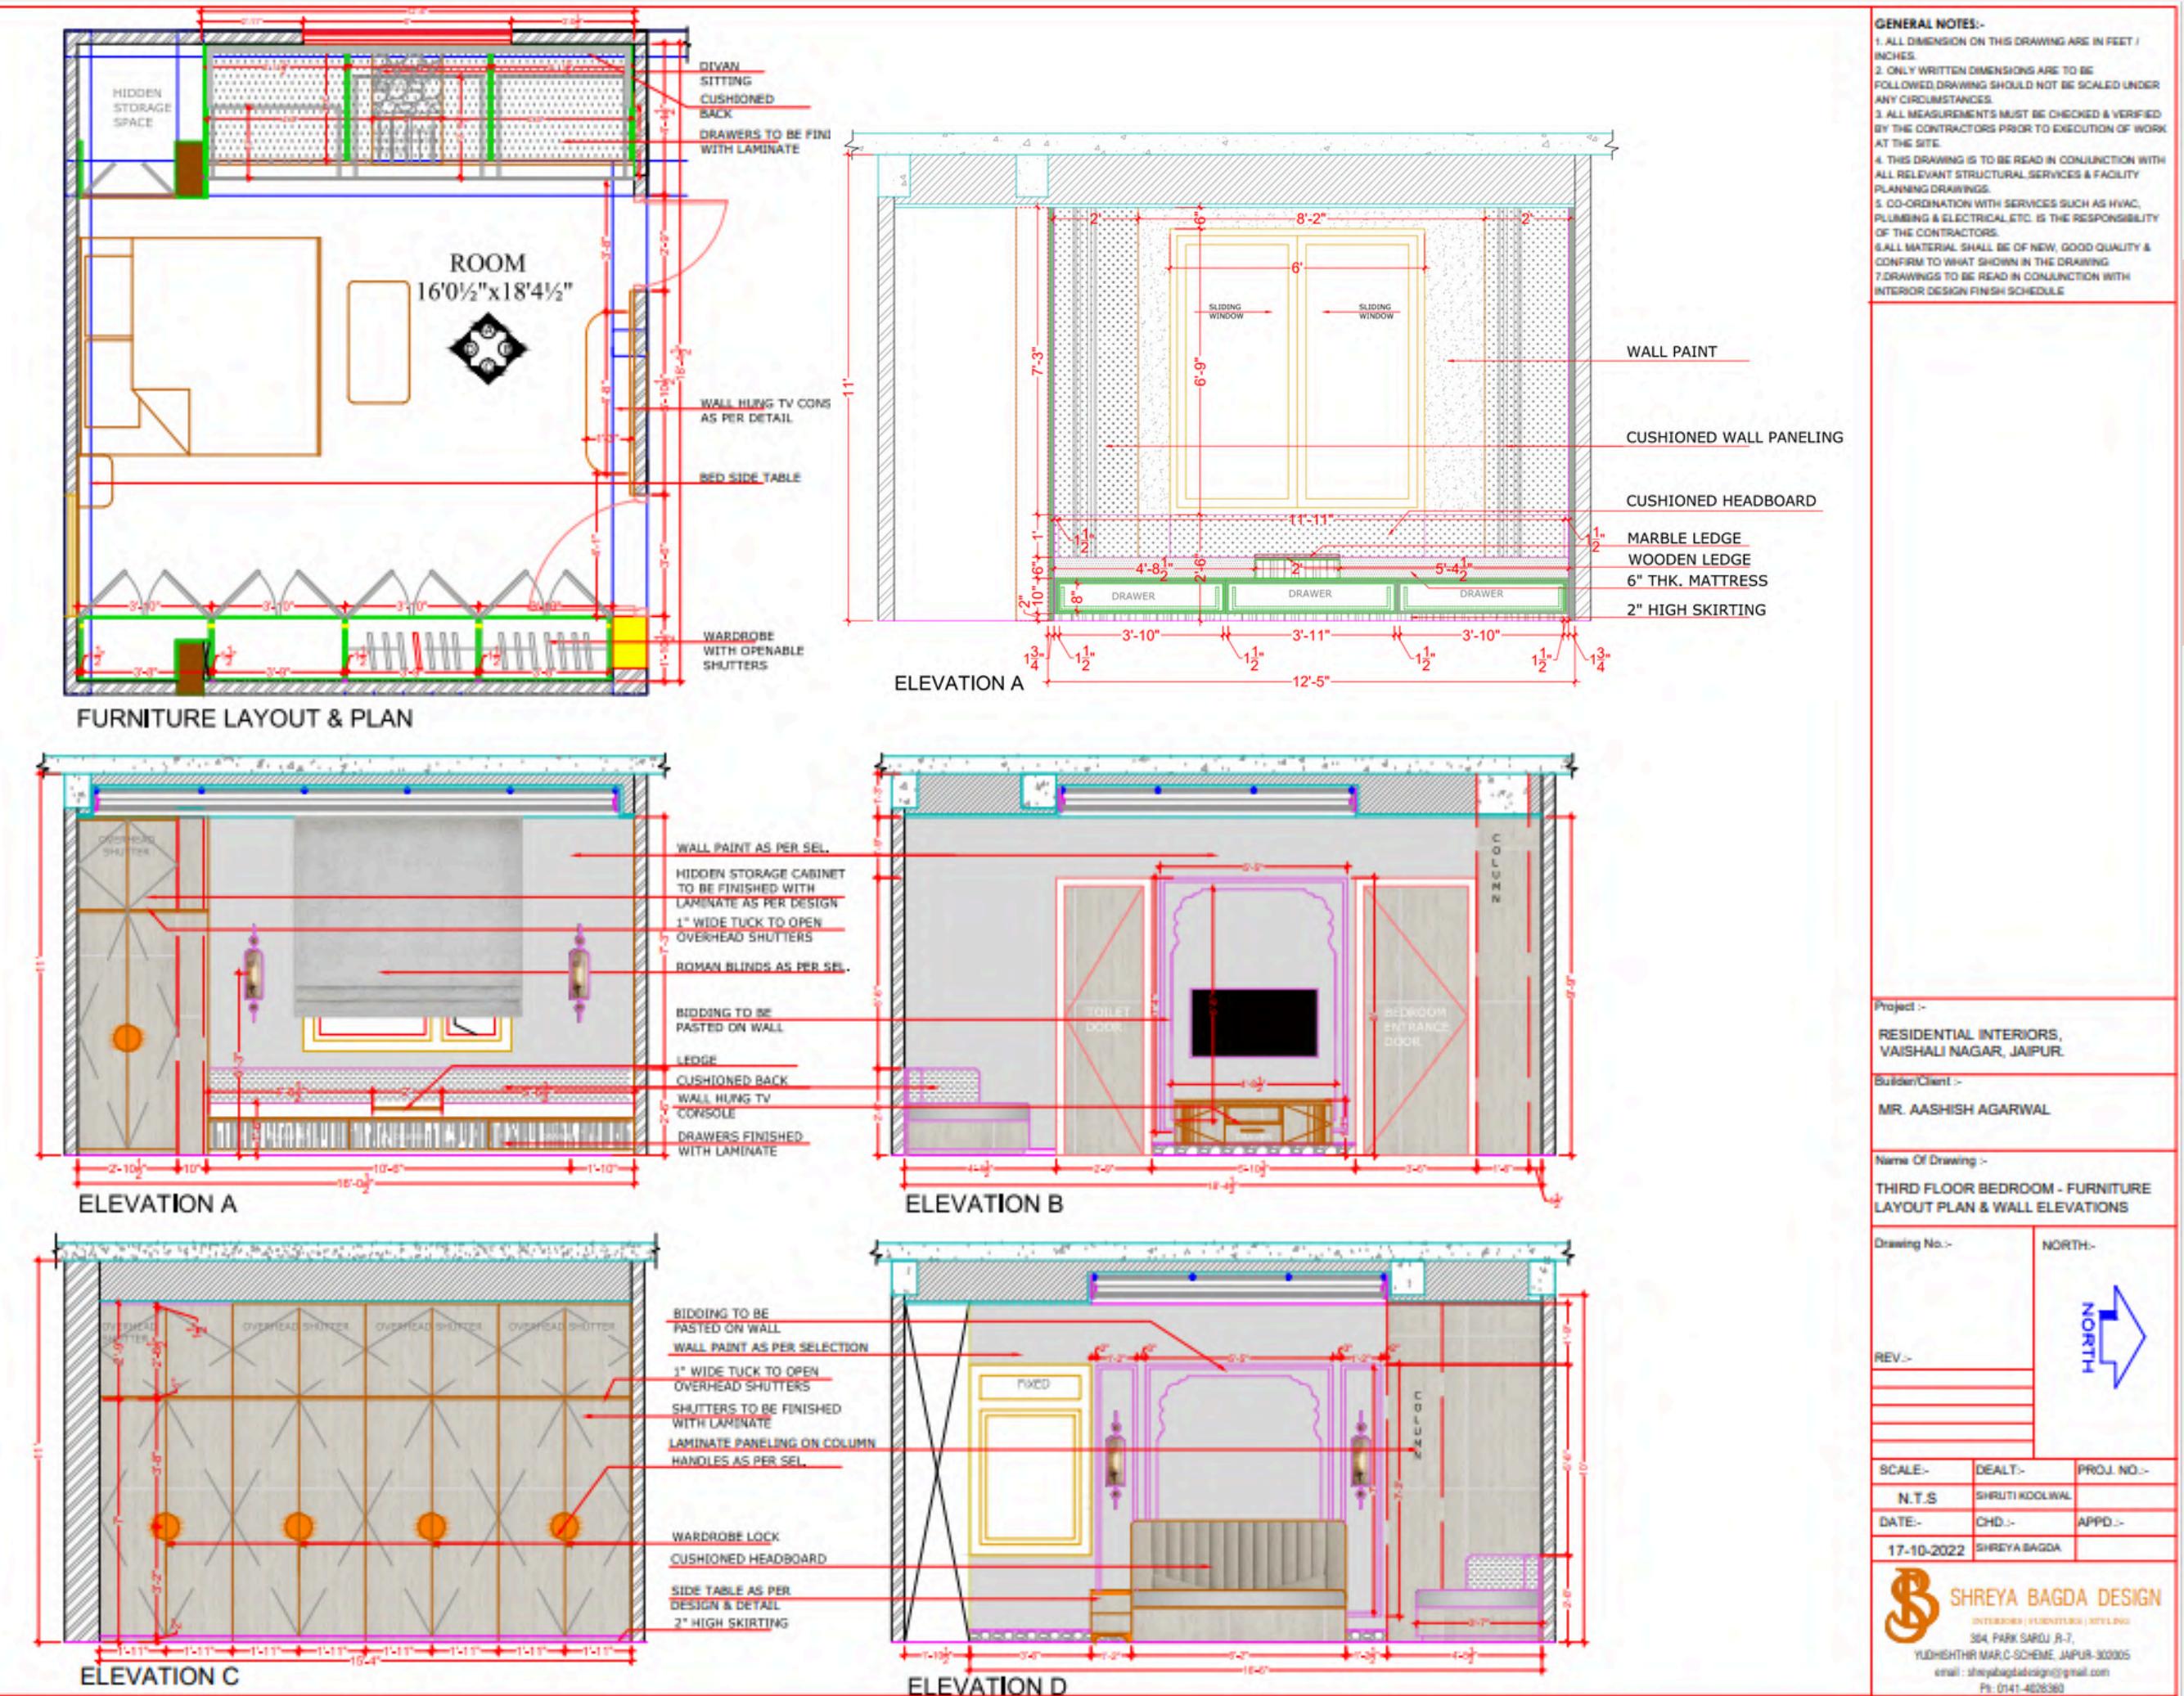



## Residential

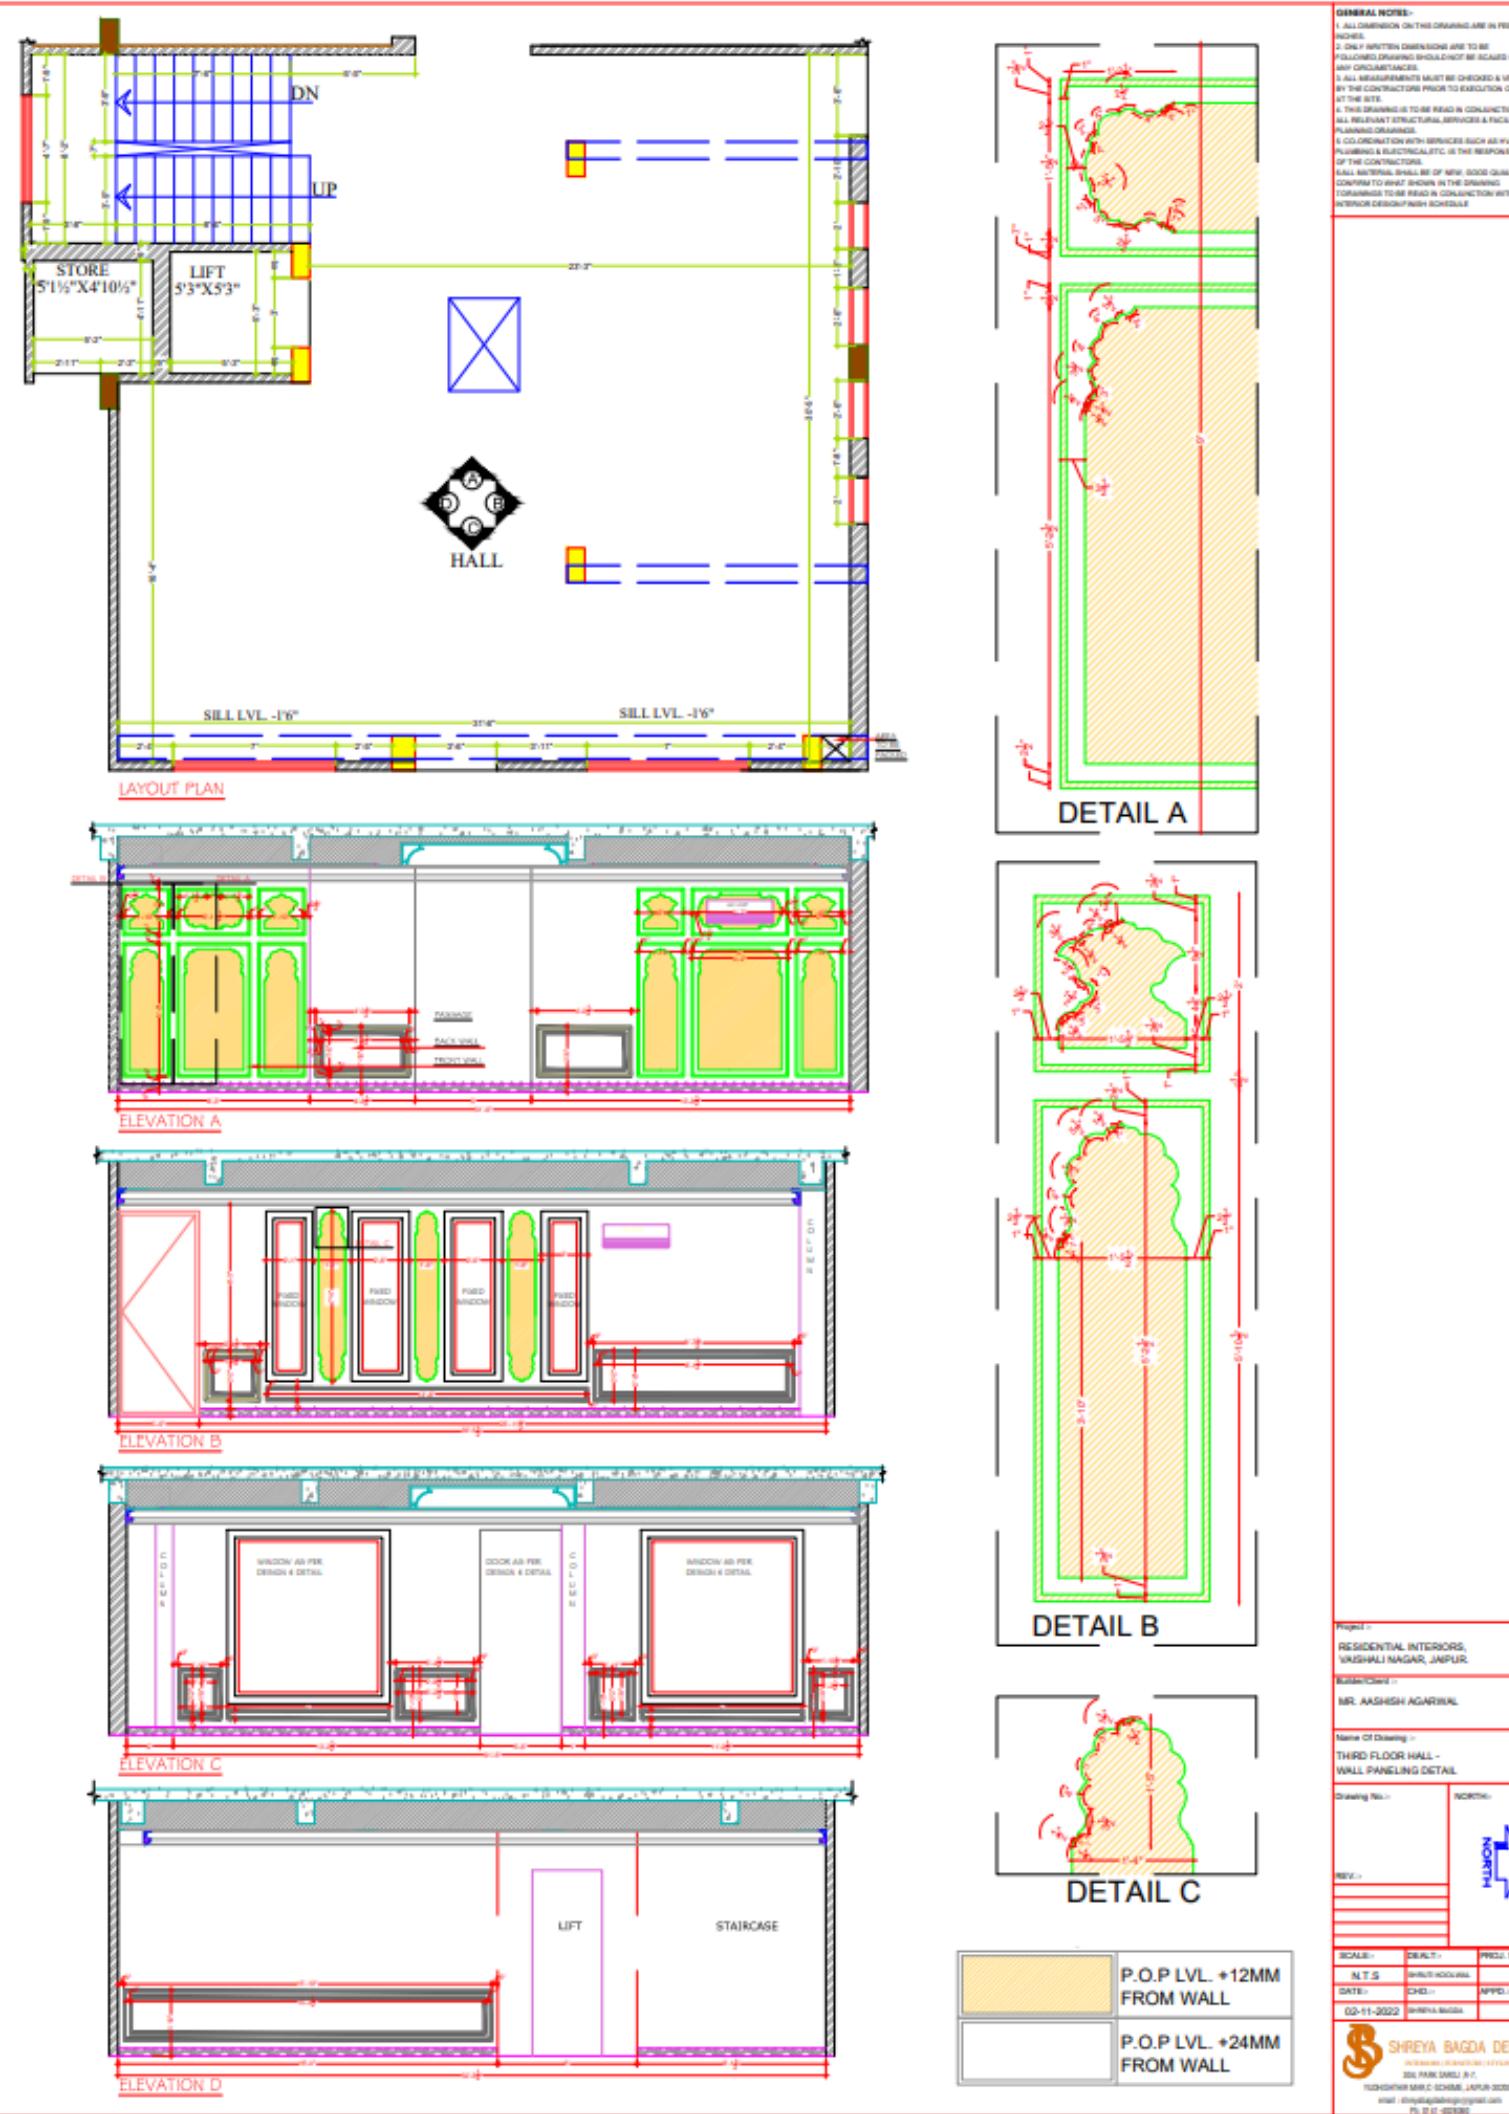


## Hall Wall Paneling Details

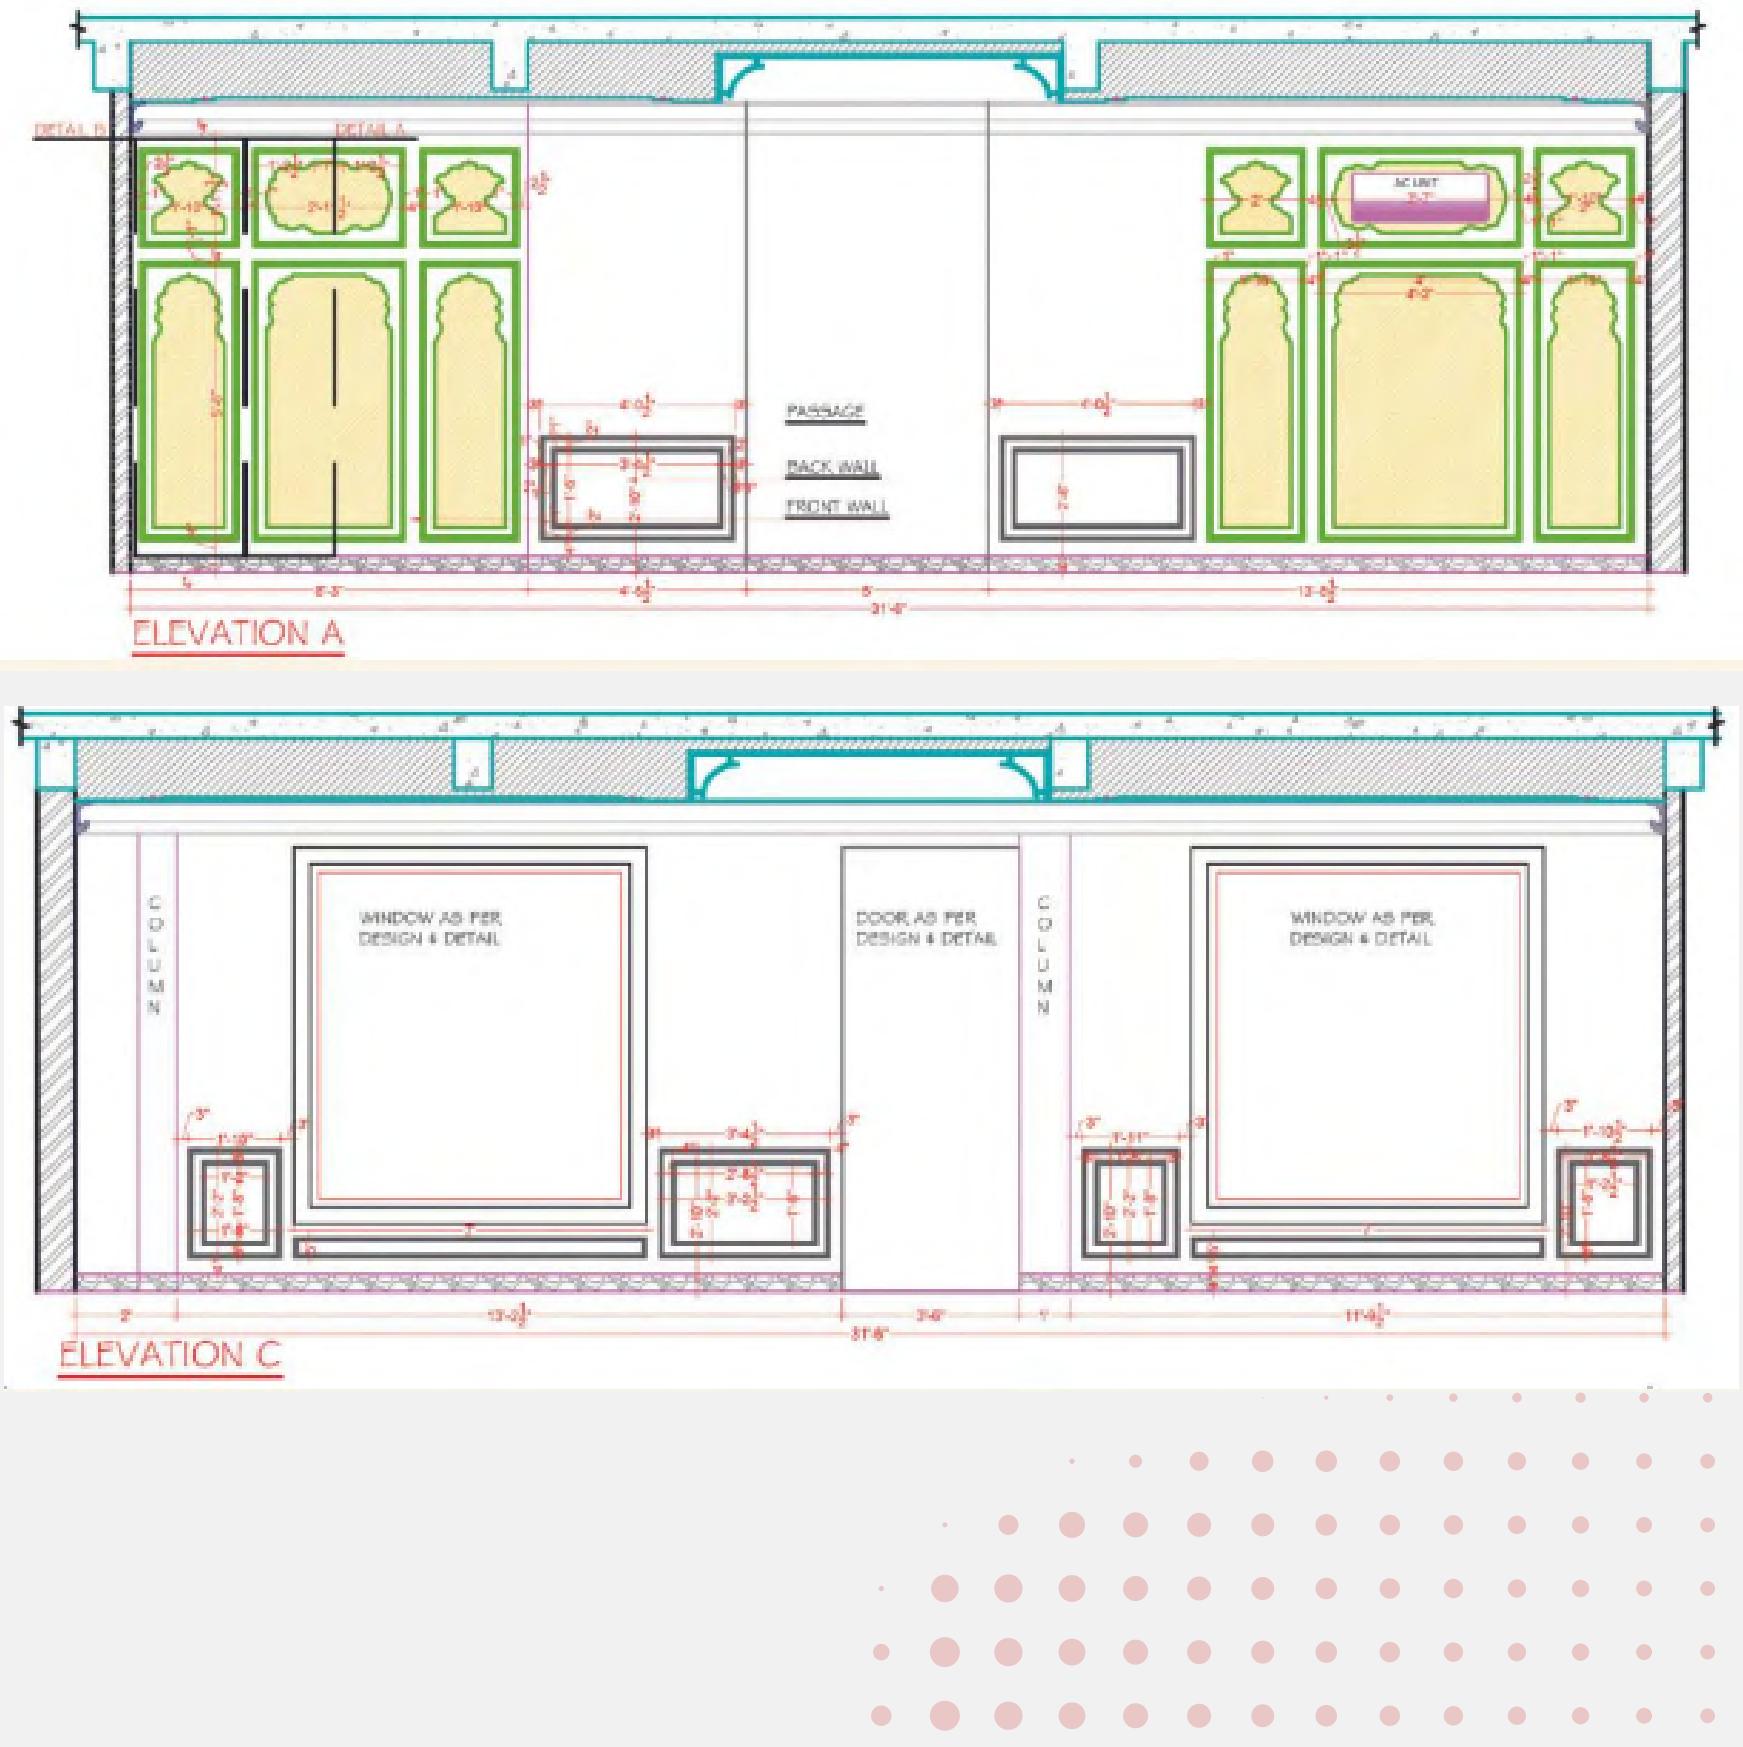

## Residential

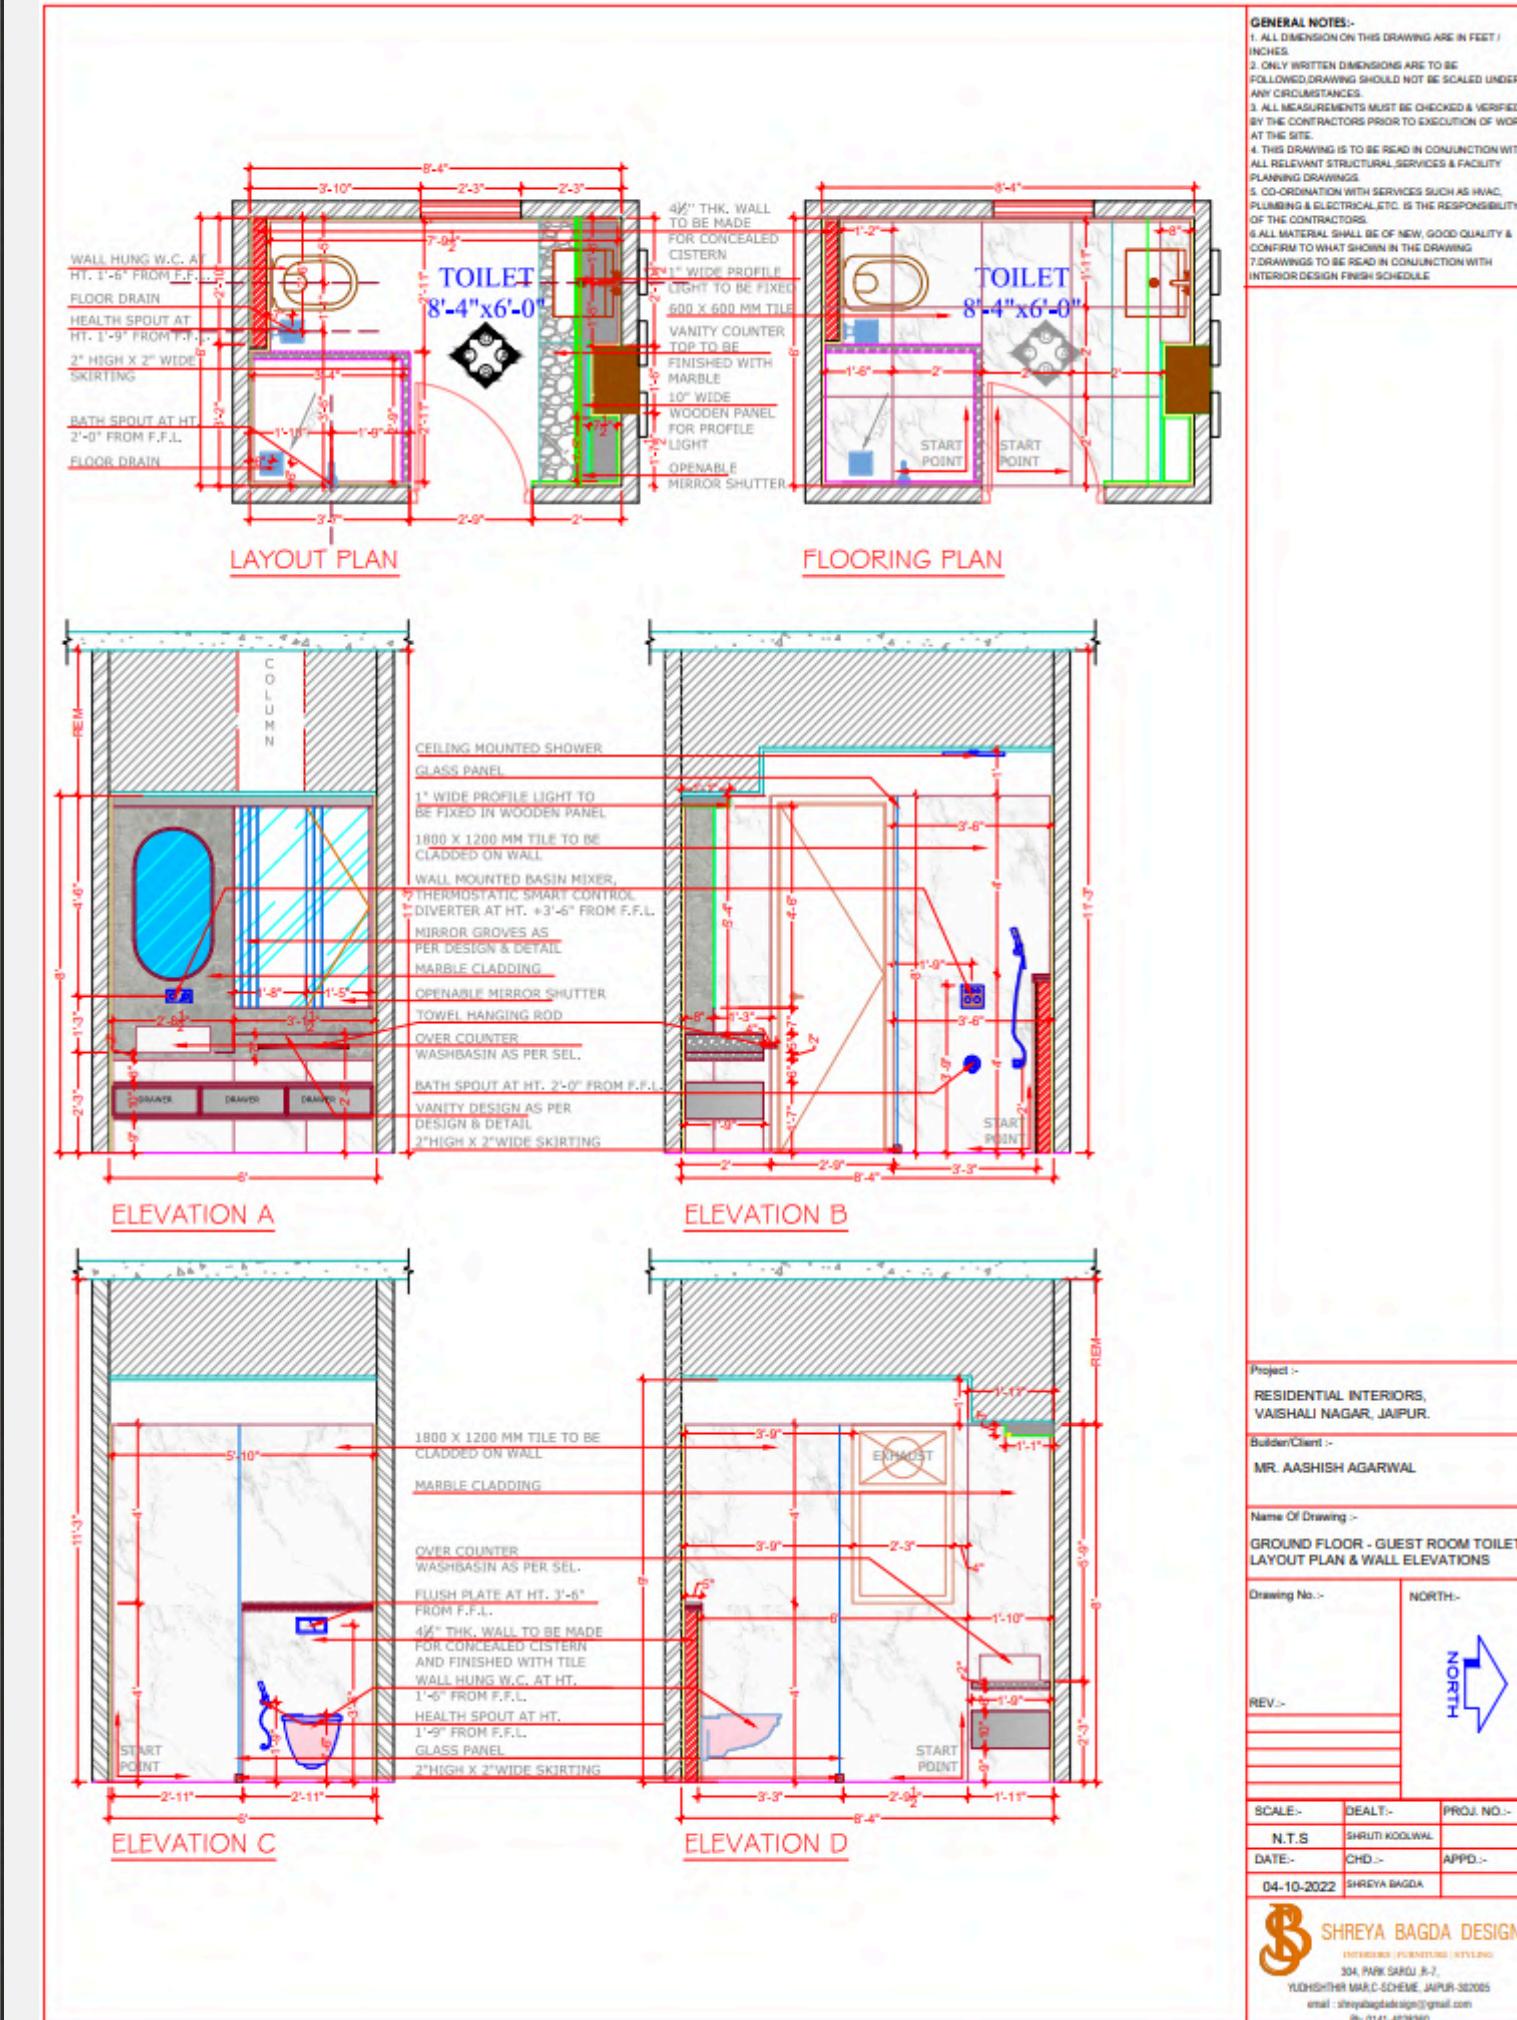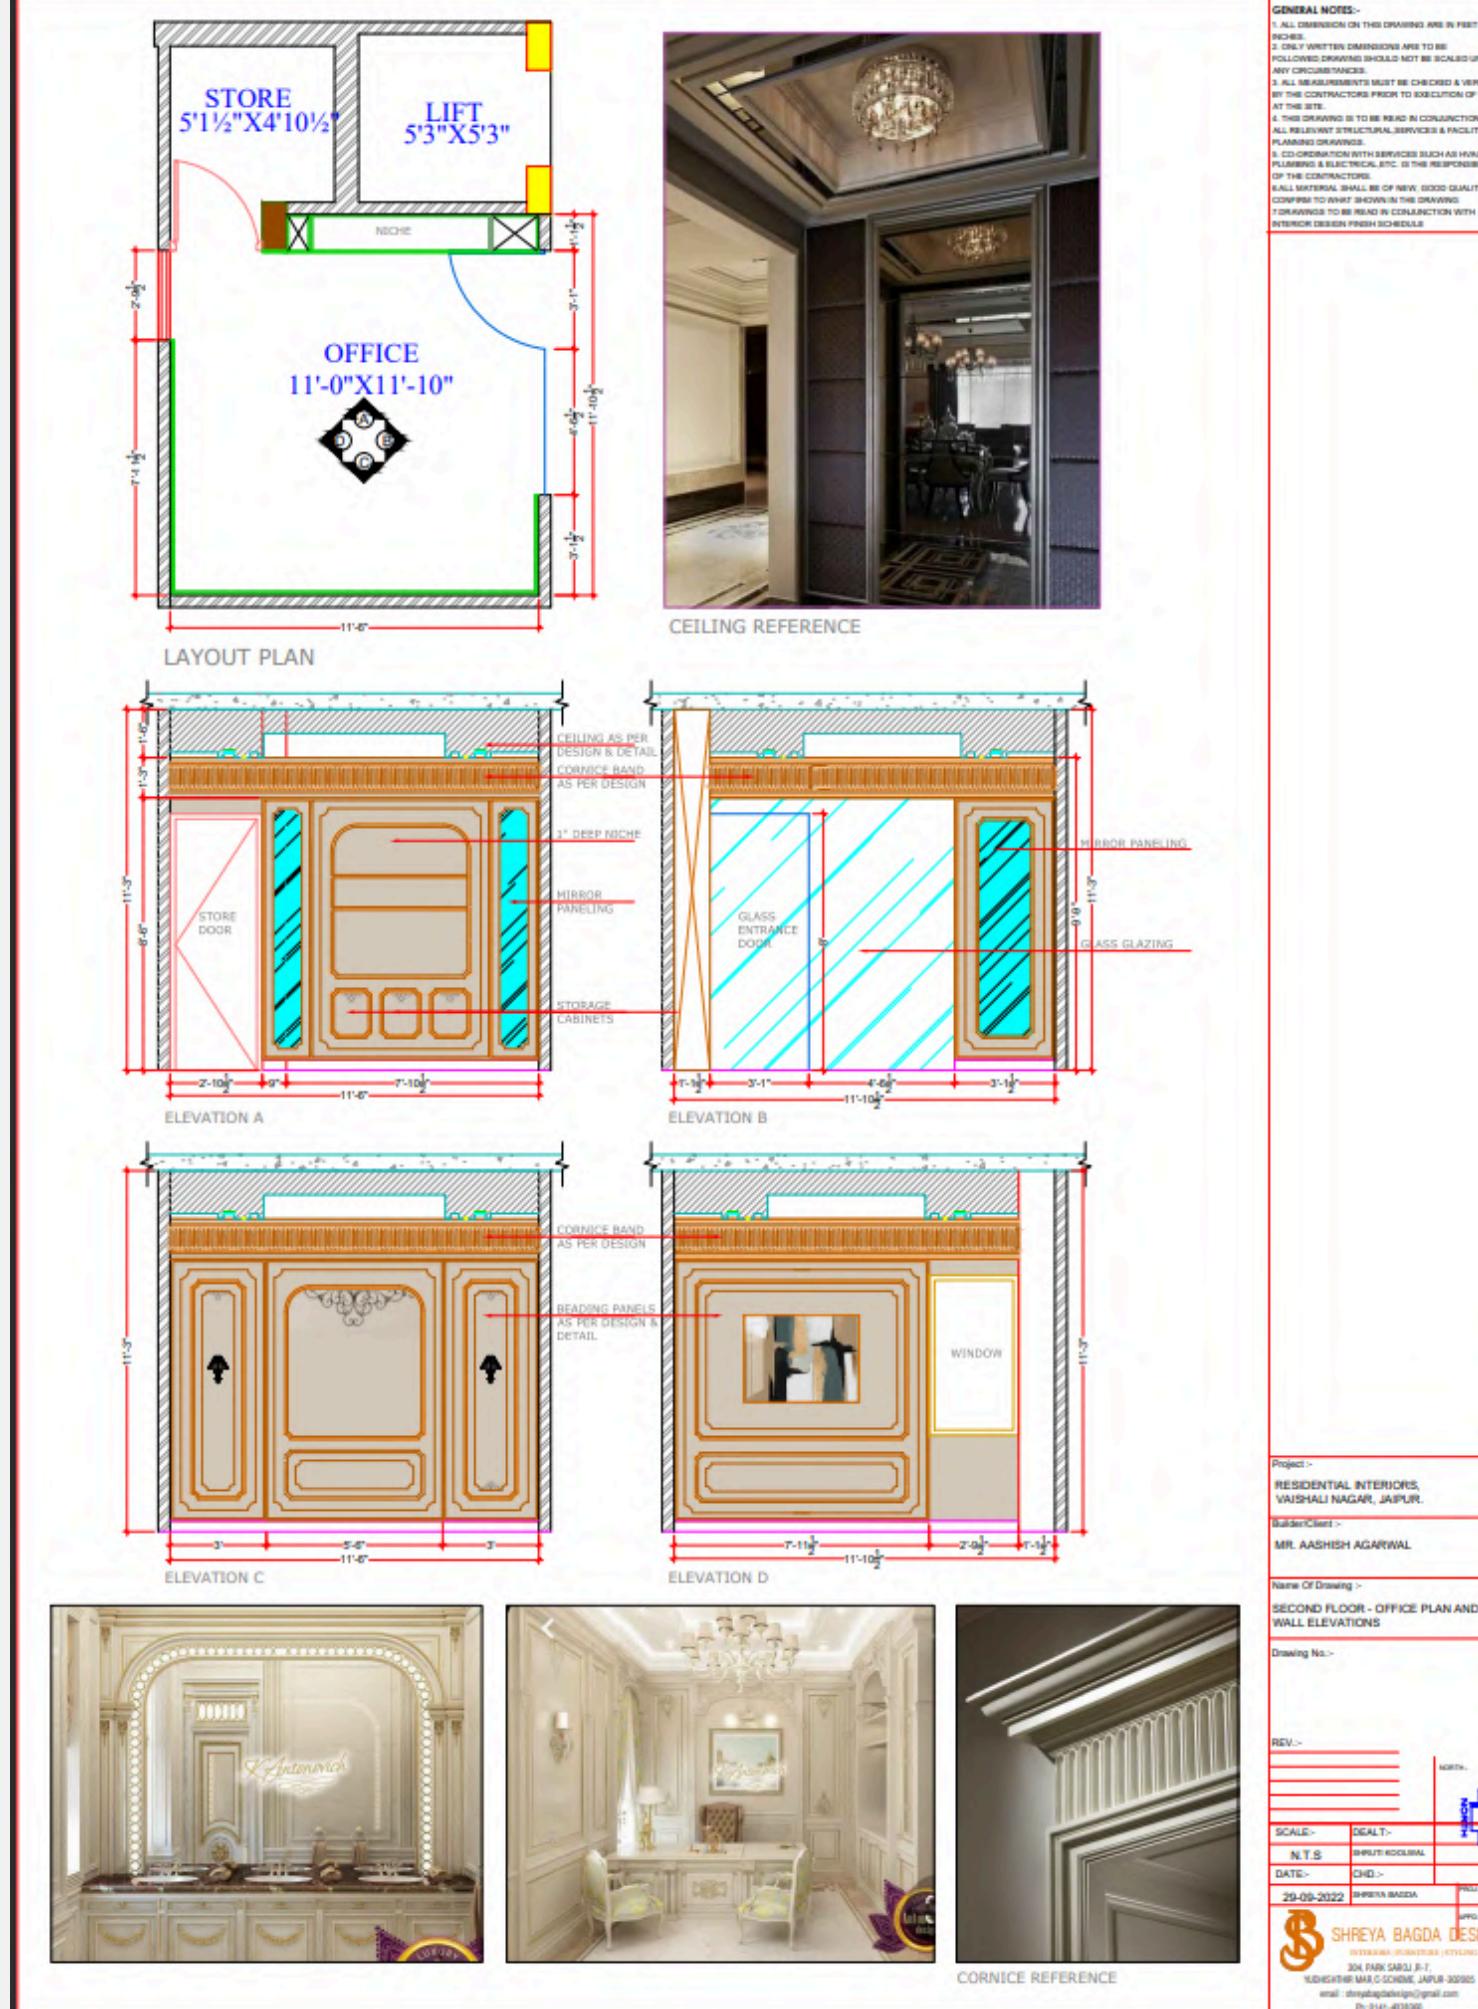

## Residential

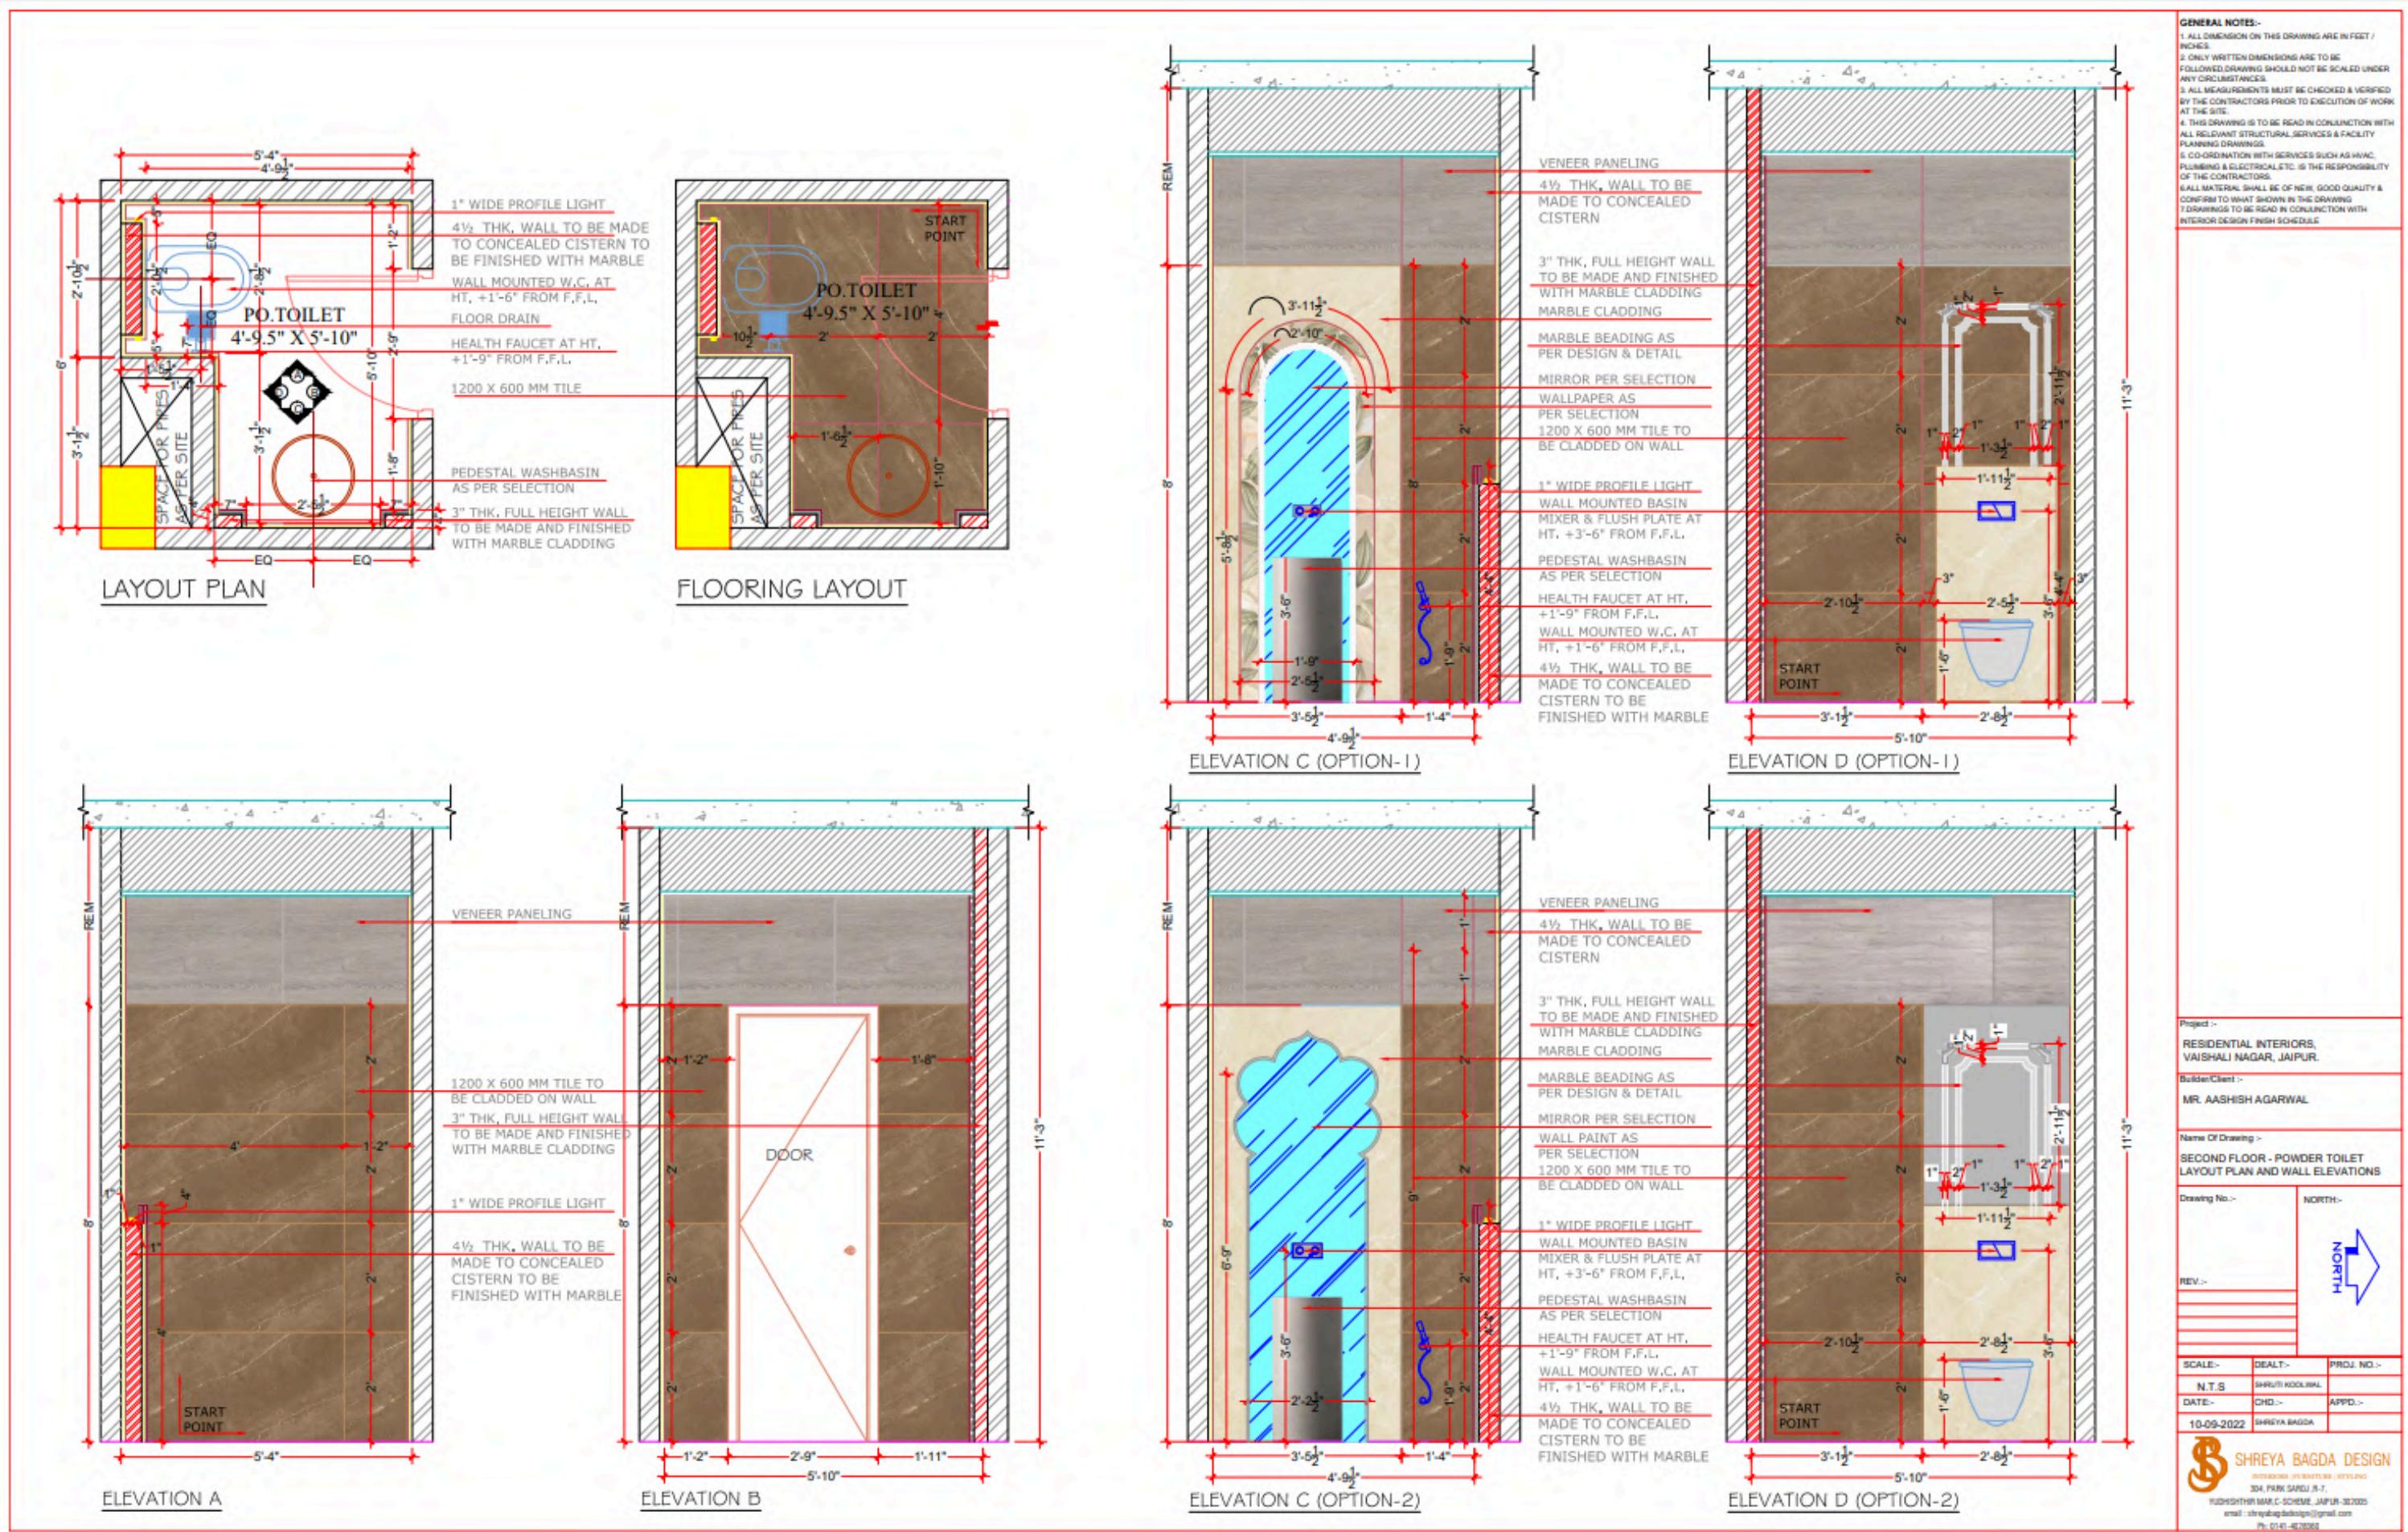

# Ajay Villa



Location – Mangal Vihar Colony,  
Gopal Pura Bypass, Jaipur, Rajasthan.  
Area – 1600 sq. ft.

- This project is a G+2 Storey House having 4 Bedrooms. The Ground Floor consists of the owner's workstation.
- On the First Floor living cum guest room adjoining the parent's bedroom, and a dining area connects all these spaces.
- On the Second Floor there are 2 bedrooms (the master's, and the sons' room) with an open balcony attached to the hall.
- On the Terrace floor they have a bedroom along with an entertainment room, with a common bathroom in the middle.



# Residential

## Bathroom Ceiling Detail

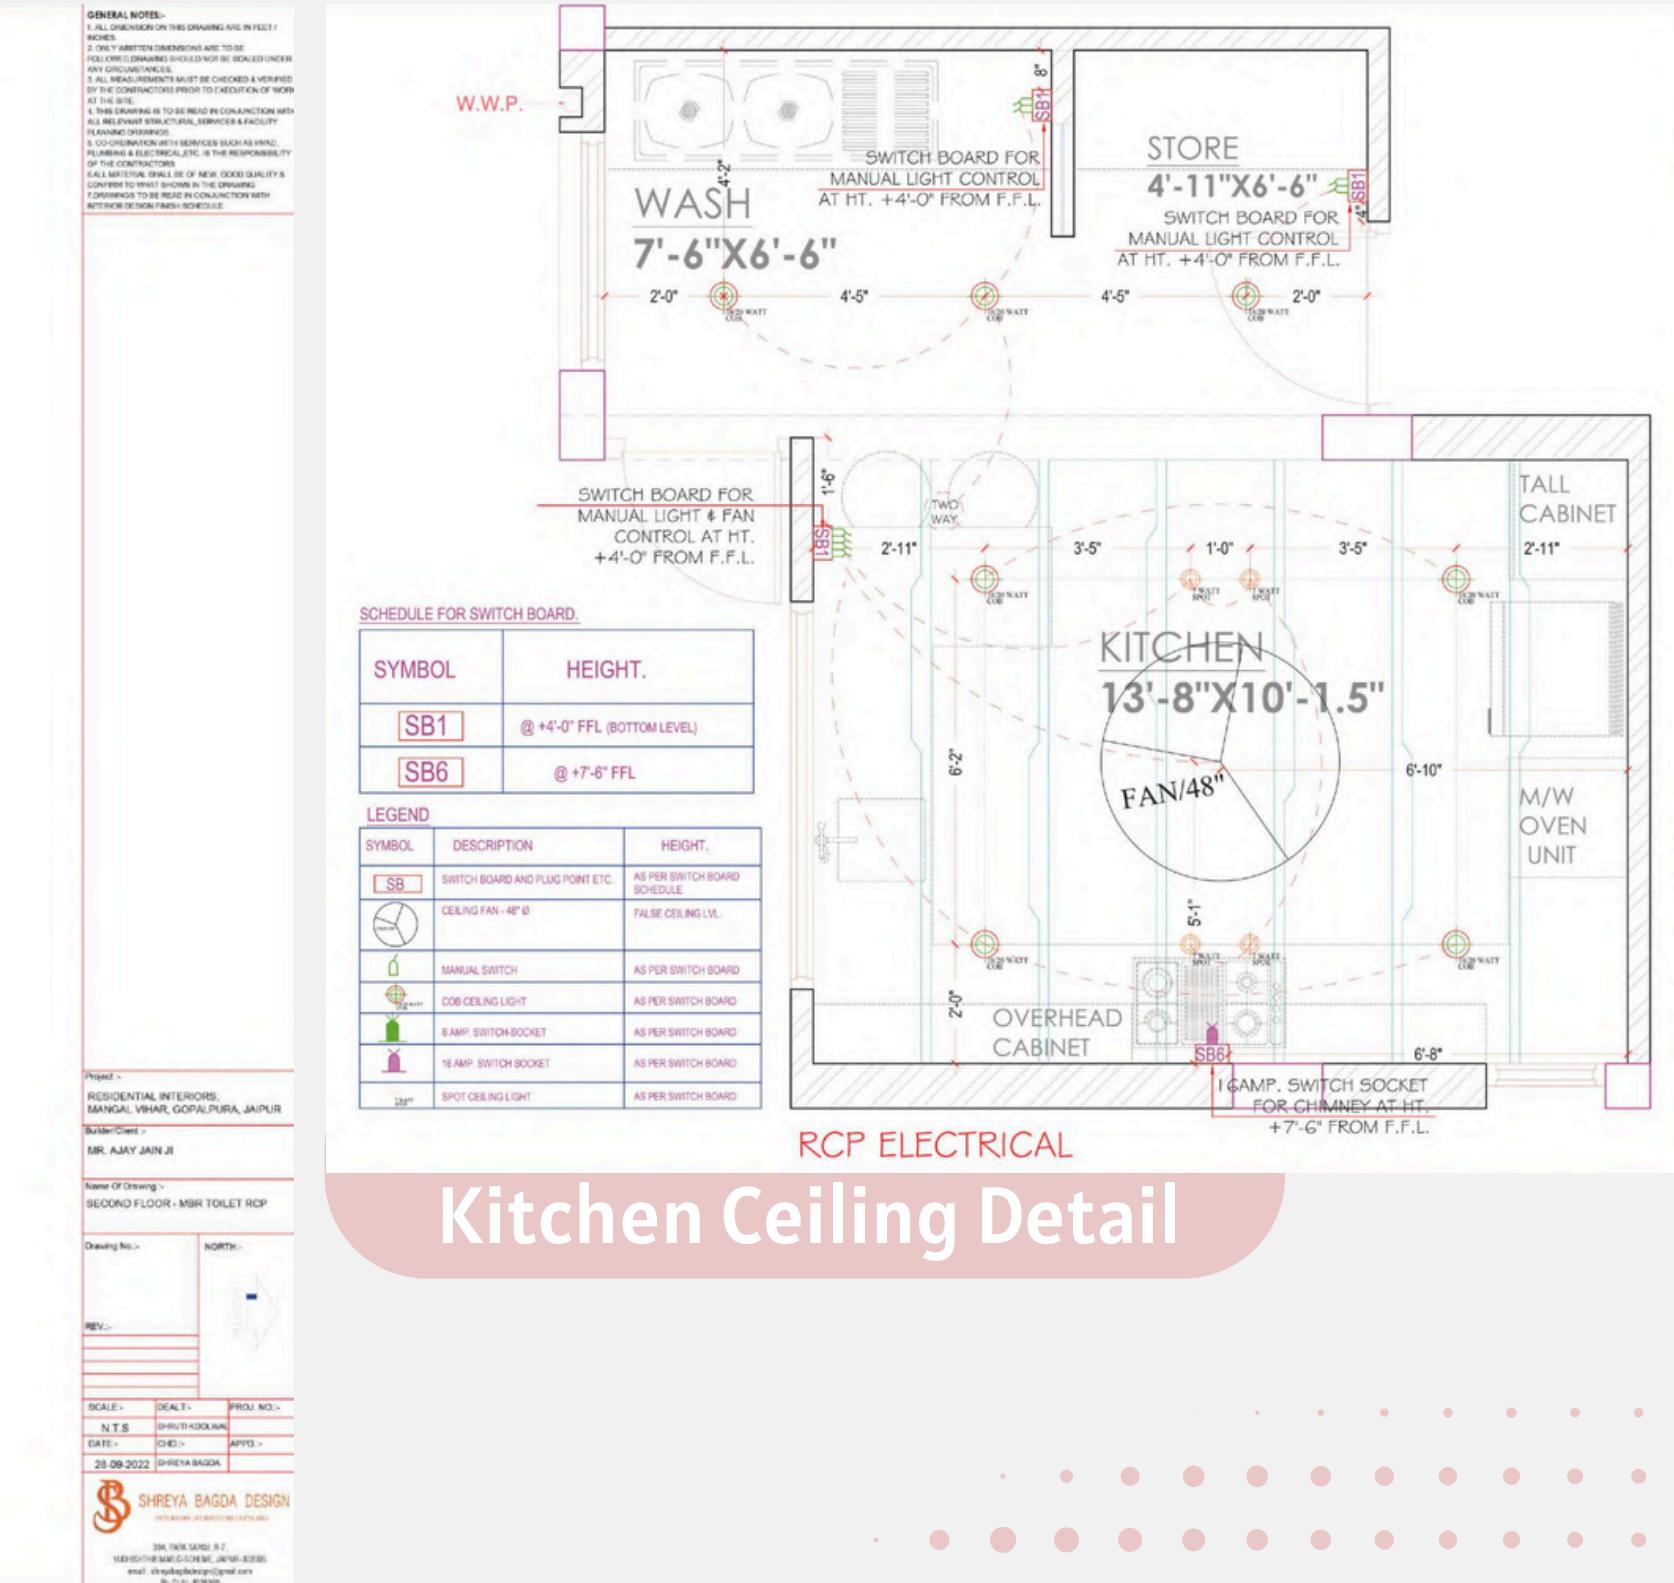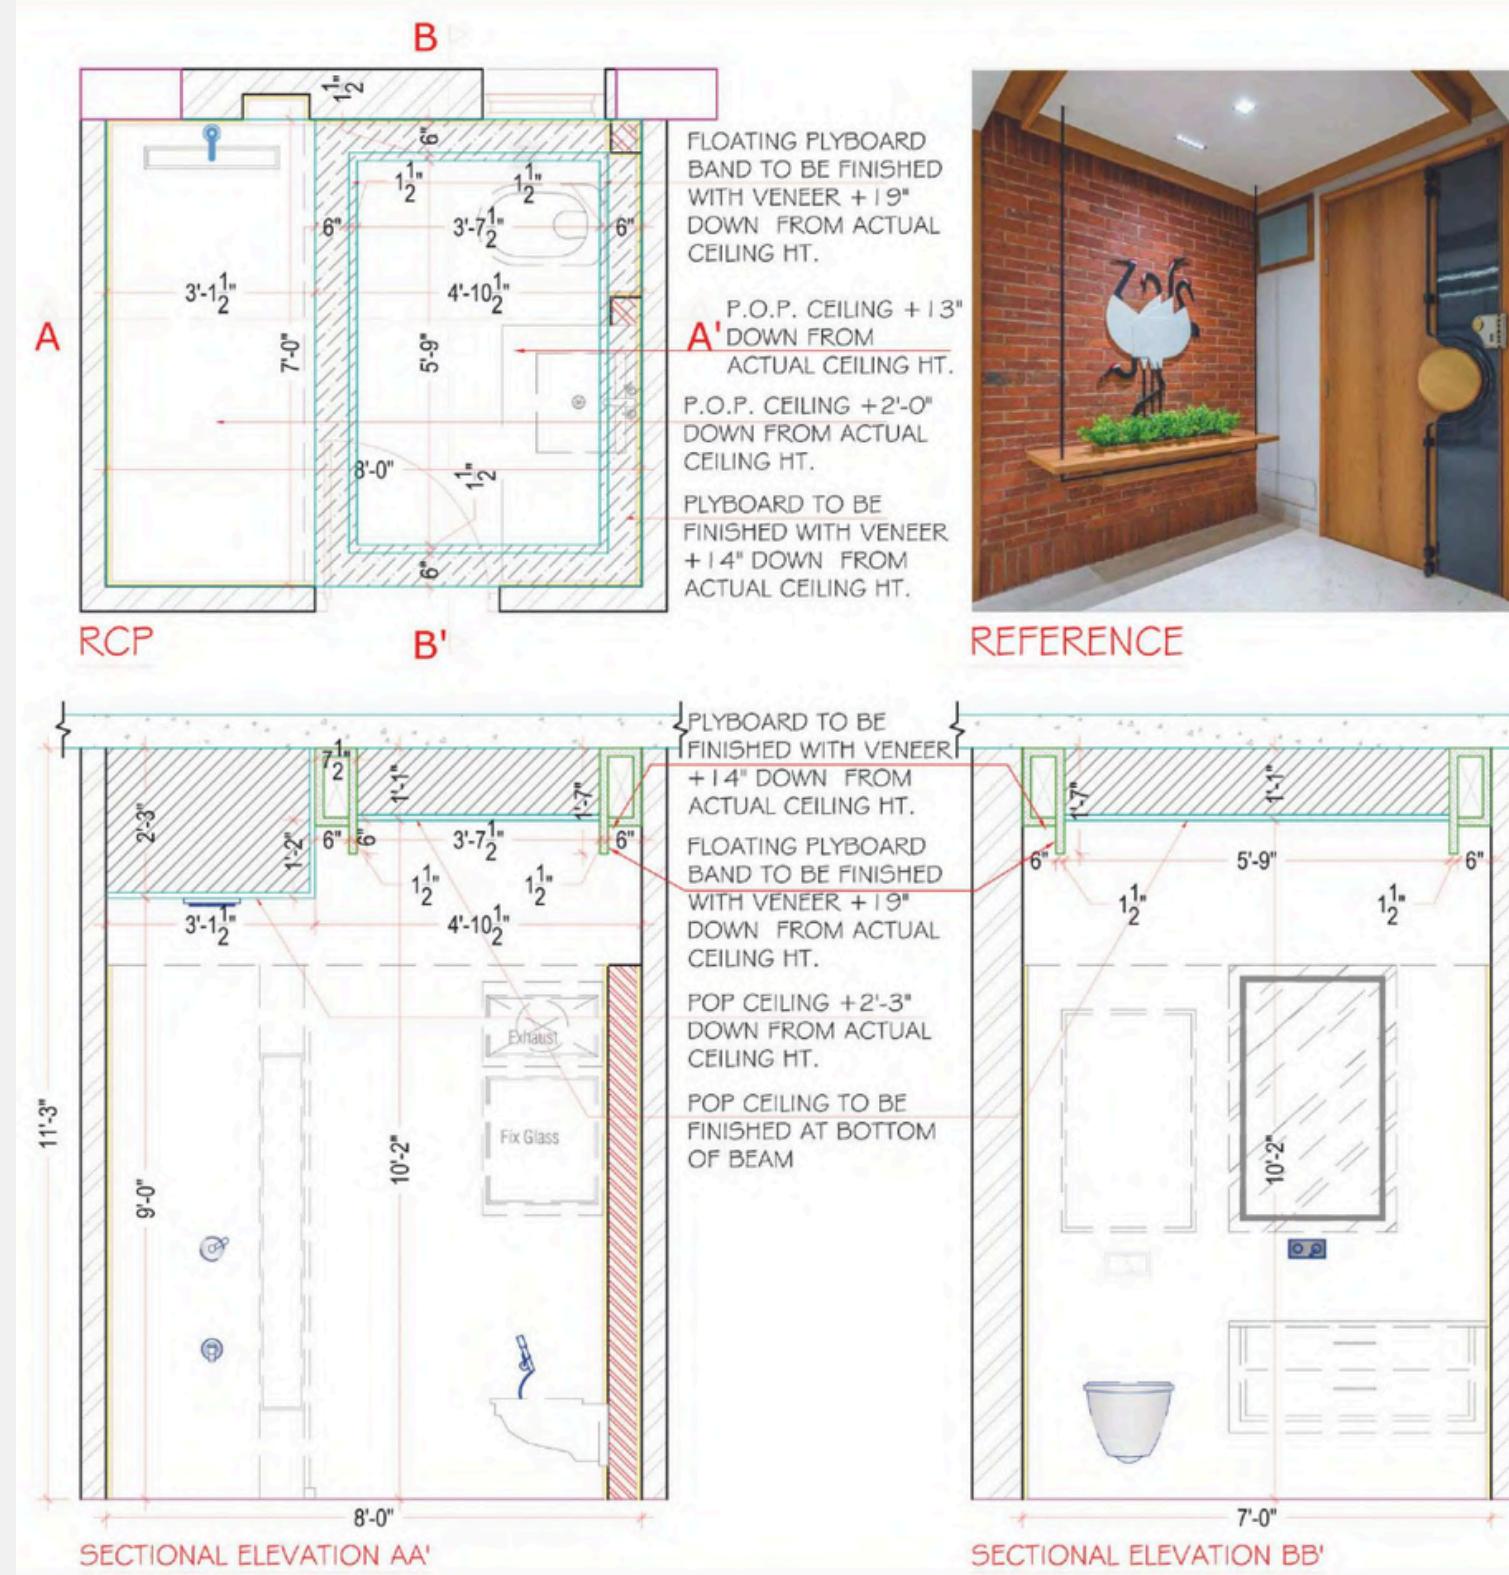


Location - 801, Somdatt Landmark,  
Hawa Sadak, Jaipur, Rajasthan.


Area – 2600 sq. ft. (one residential floor)

- This project is a 4BHK Apartment along with the building's Terrace owned by the client himself.
- The apartment also has a separate dining & drawing room.
- On the Terrace, there is an open kitchen along with seating areas and a luxury hall for meetings adjoining a common restroom.


### Bathroom Detailing

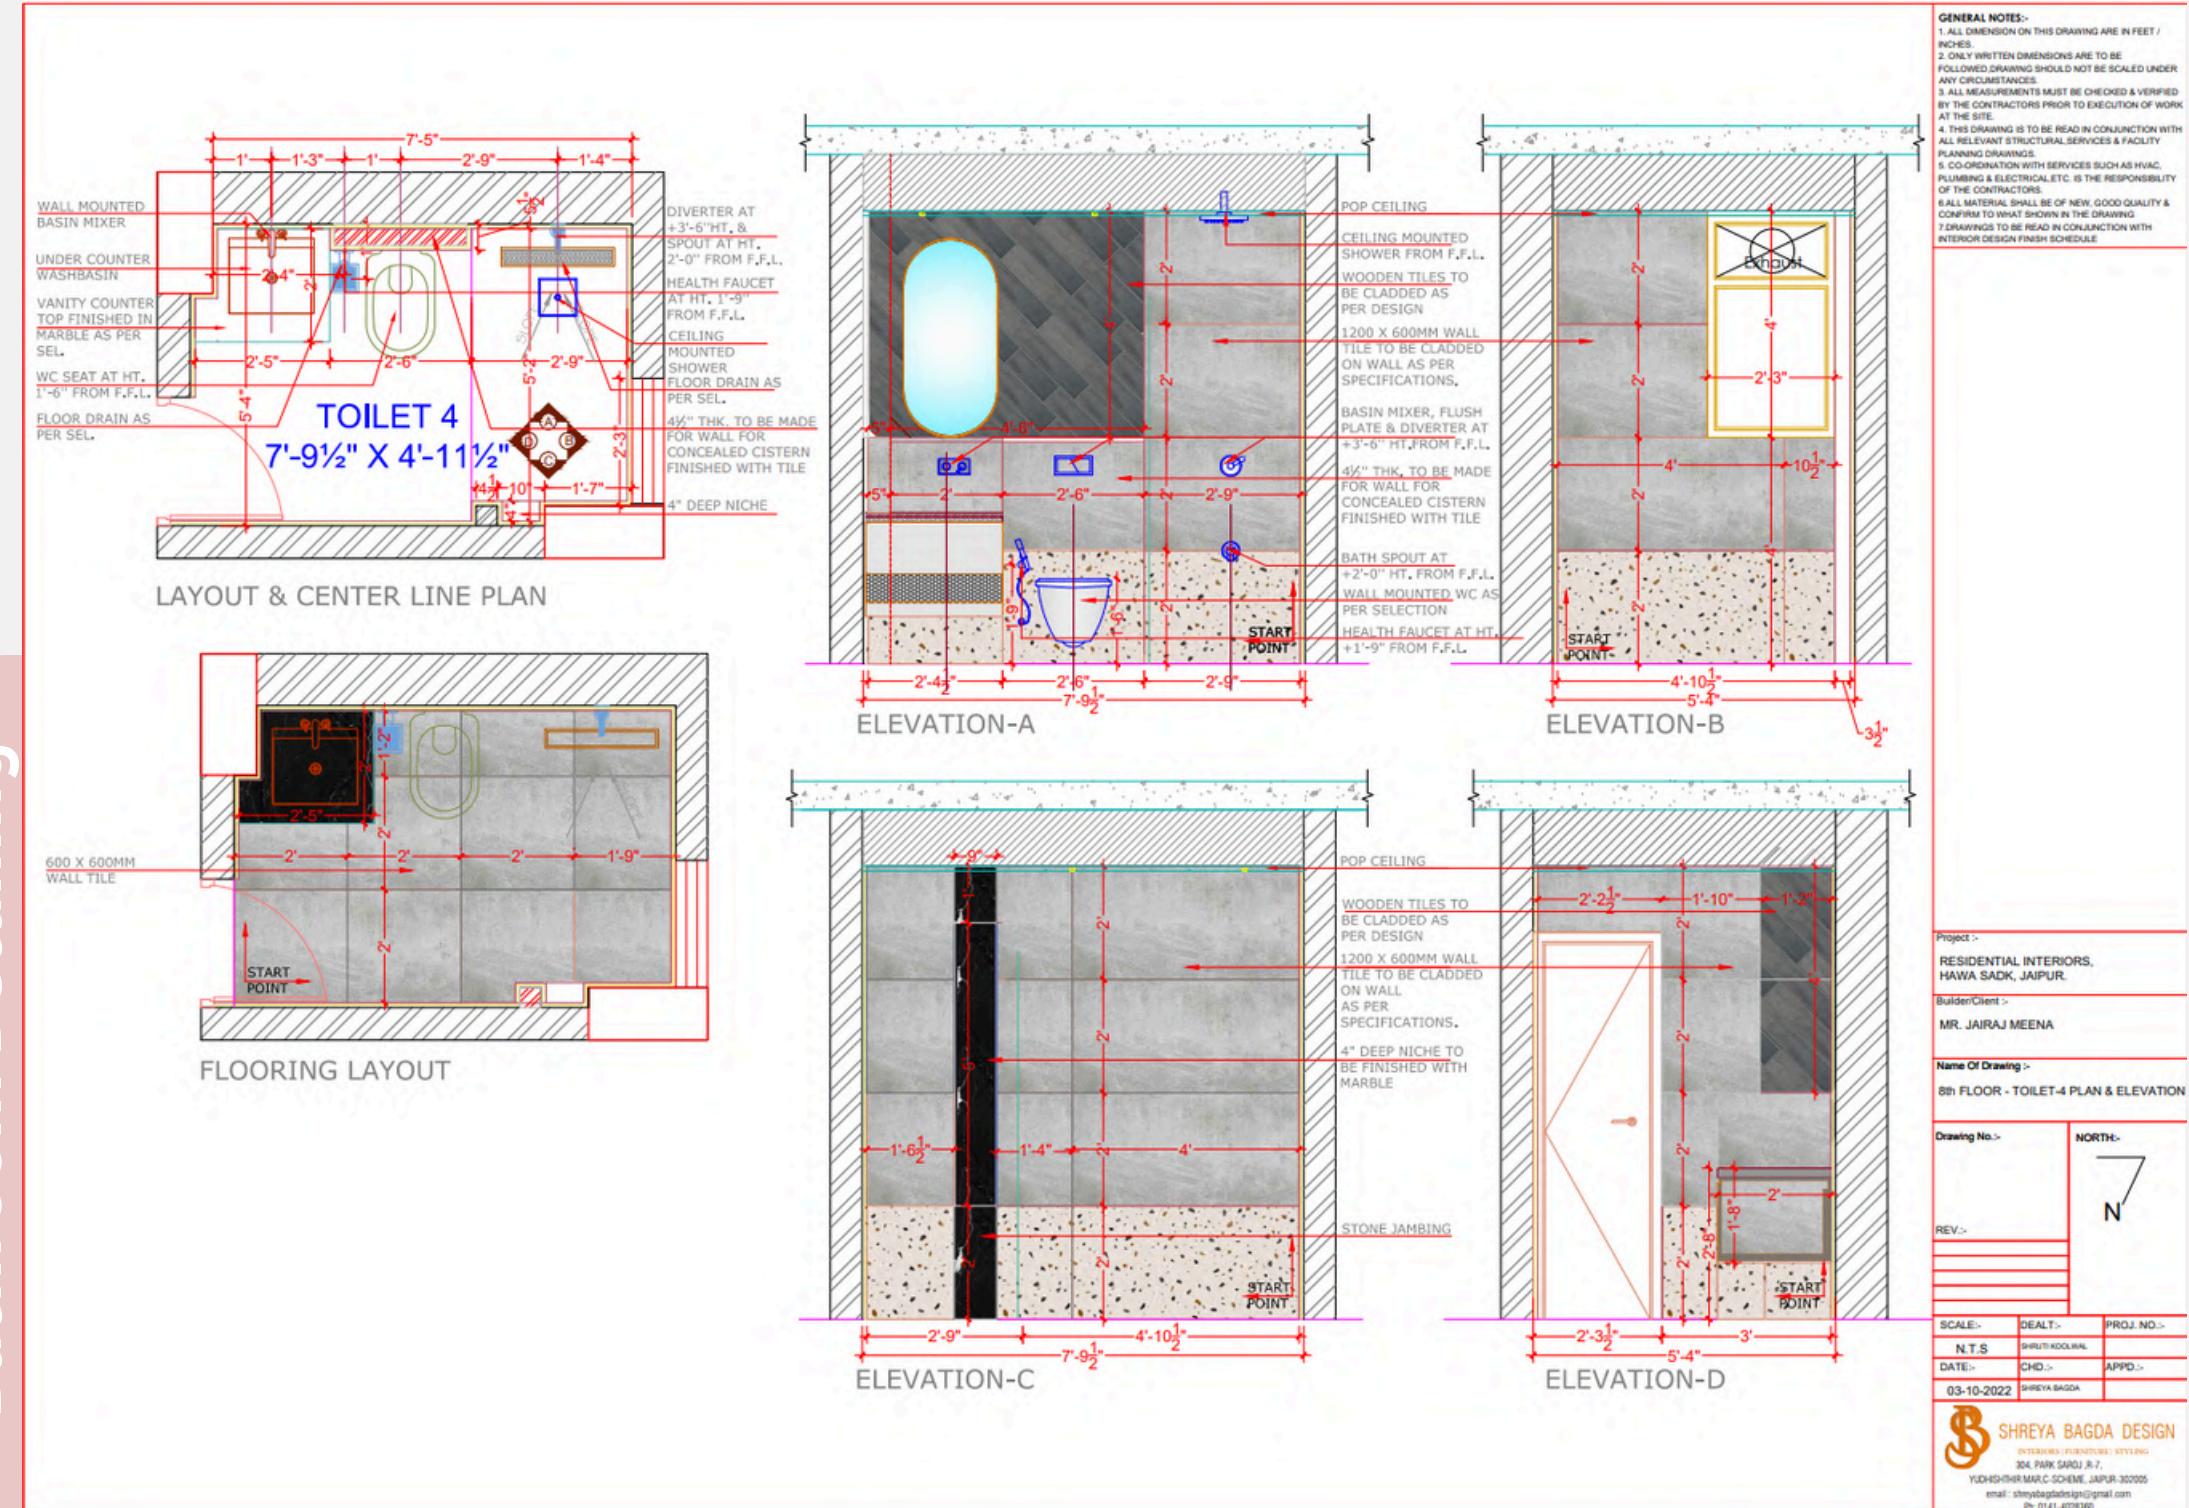

# Residential

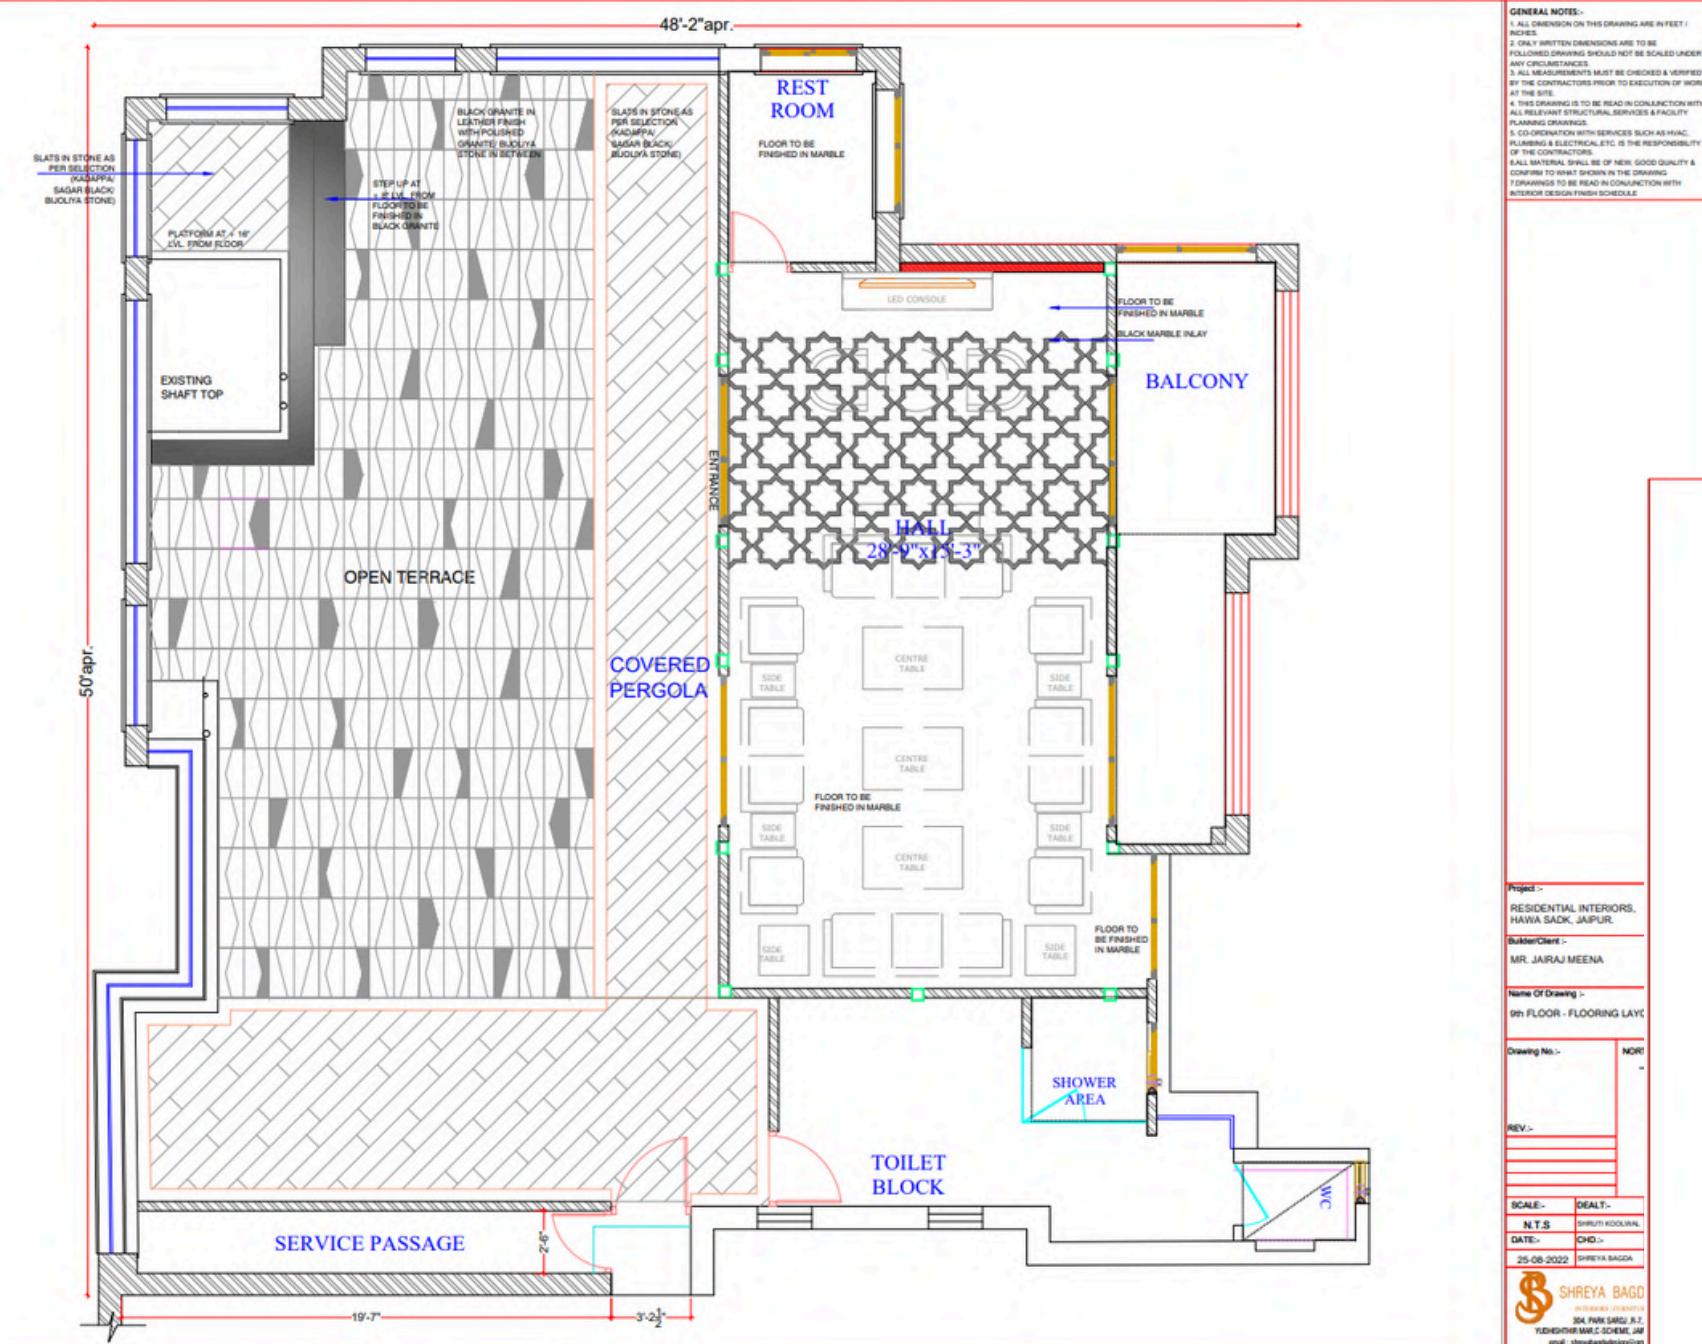


## Party Hall Flooring Detail-2

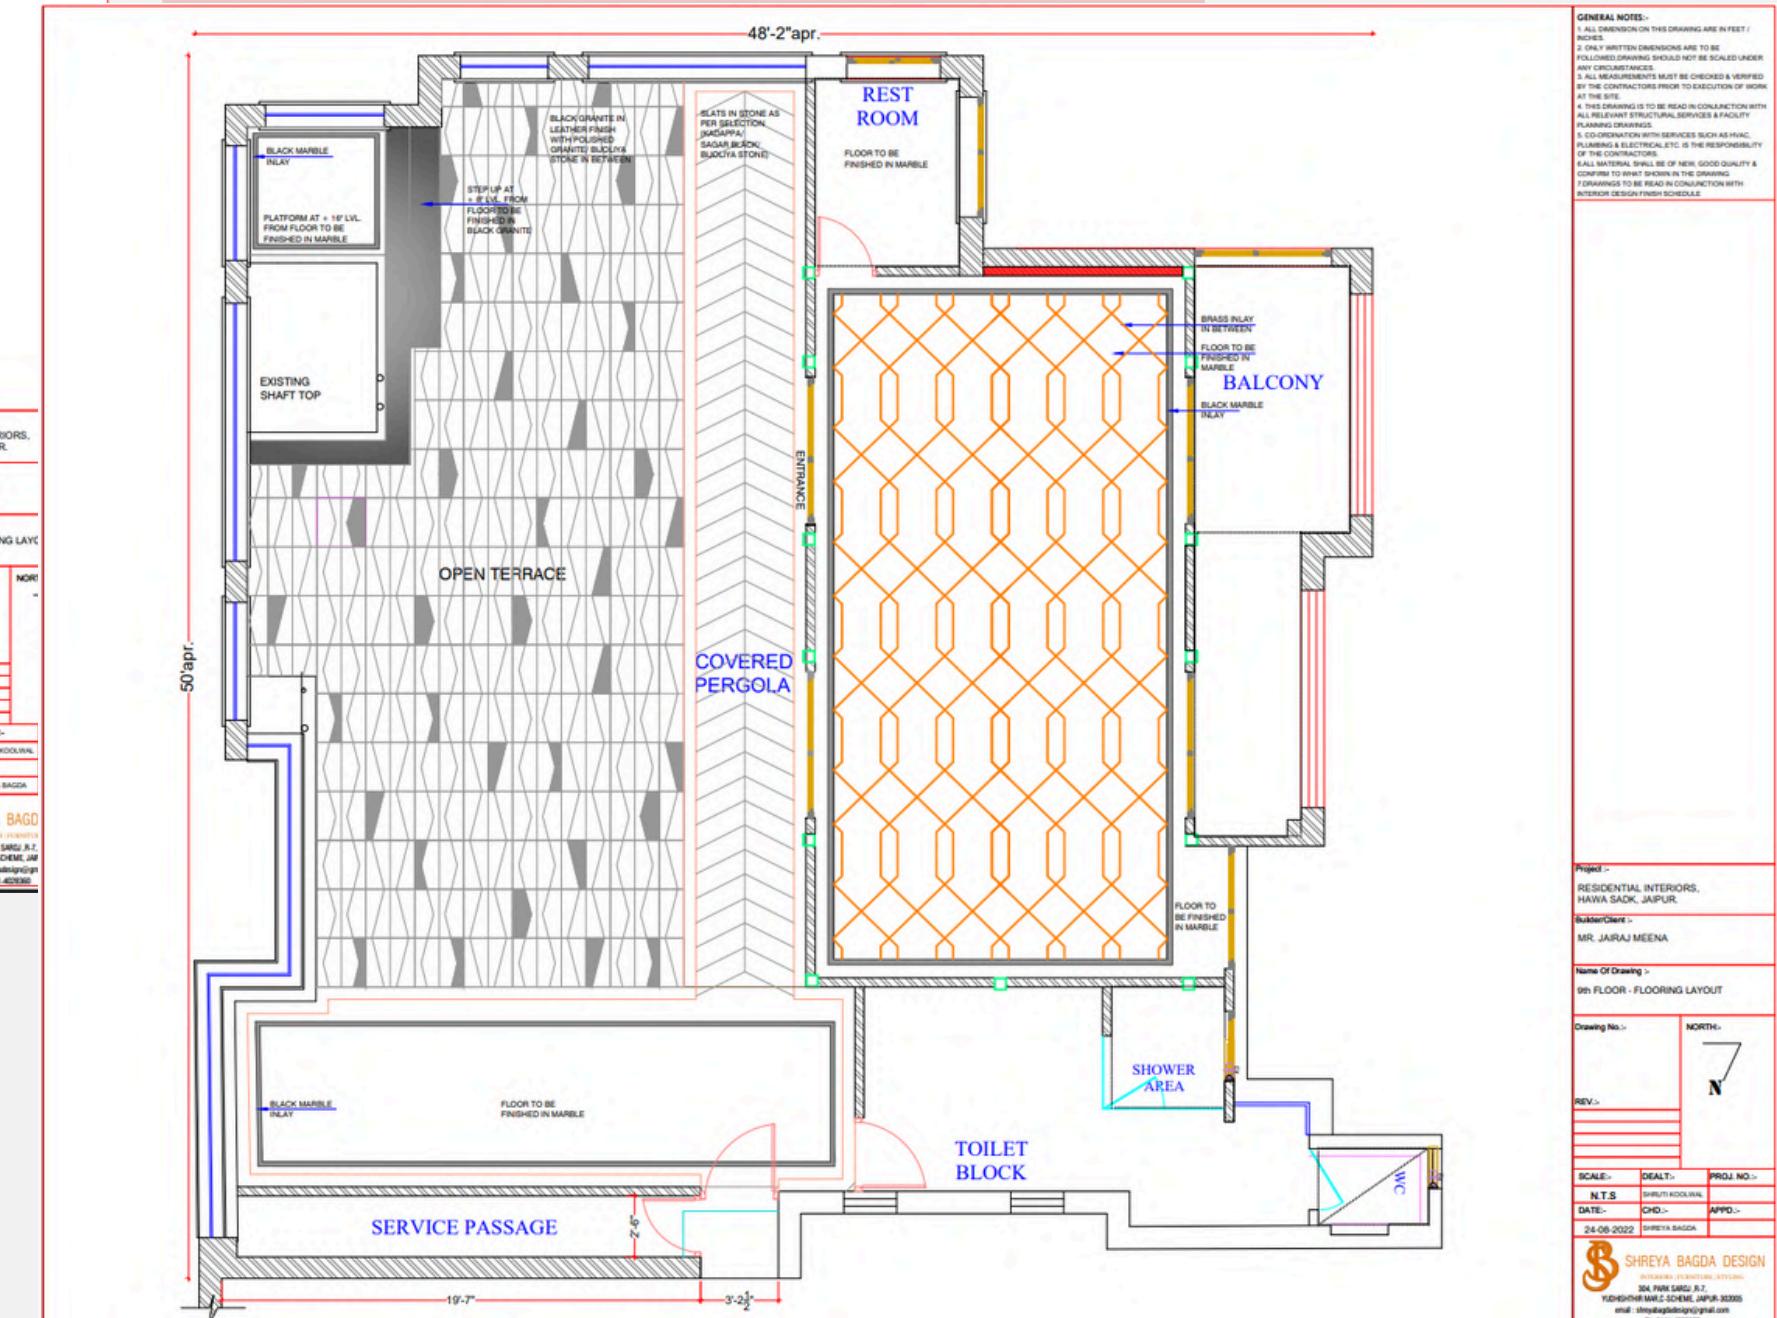

## Installed Site Images



## Installed Wardrobes

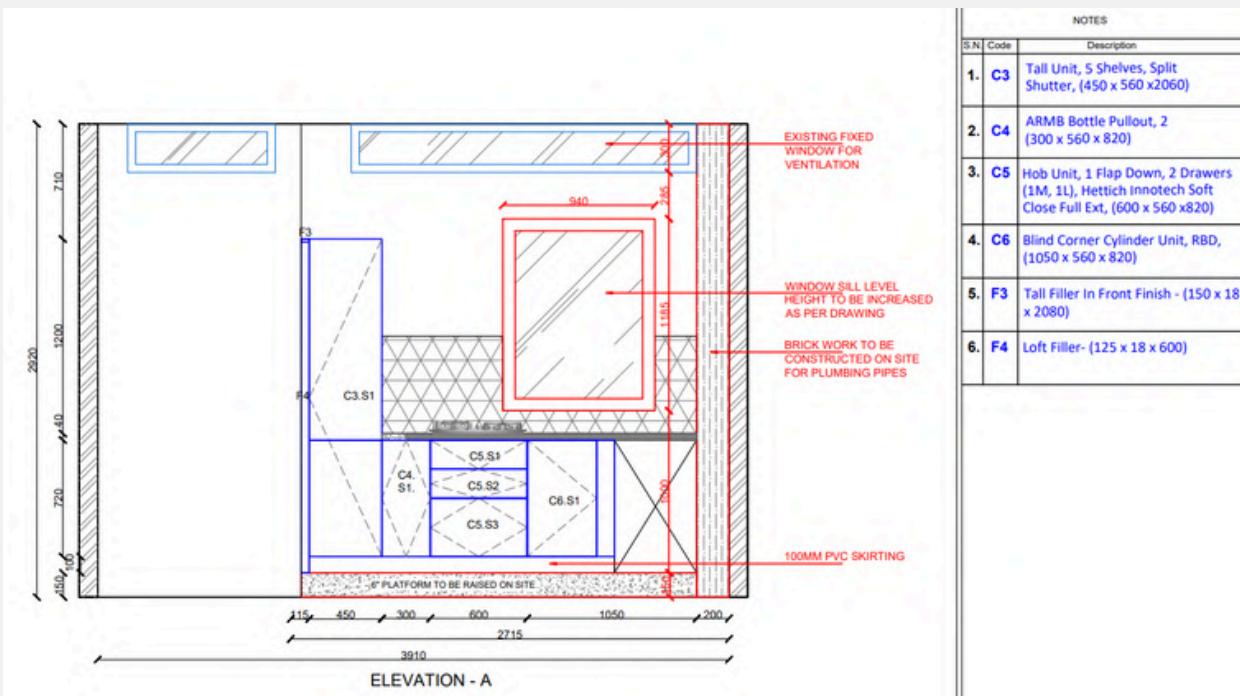

## Installed Site Images

### Installed Sites



# **THANK YOU**

**Presented By : Shruti Koolwal  
7877952953|shrutikoolwal2001@gmail.com**